


PLANO DE AERÓDROMO PARA
MOVIMIENTOS EN TIERRA-OACI

ELEV CIV APN
696 m

TWR 122.105 C
GND 121.805 C

ALBACETE

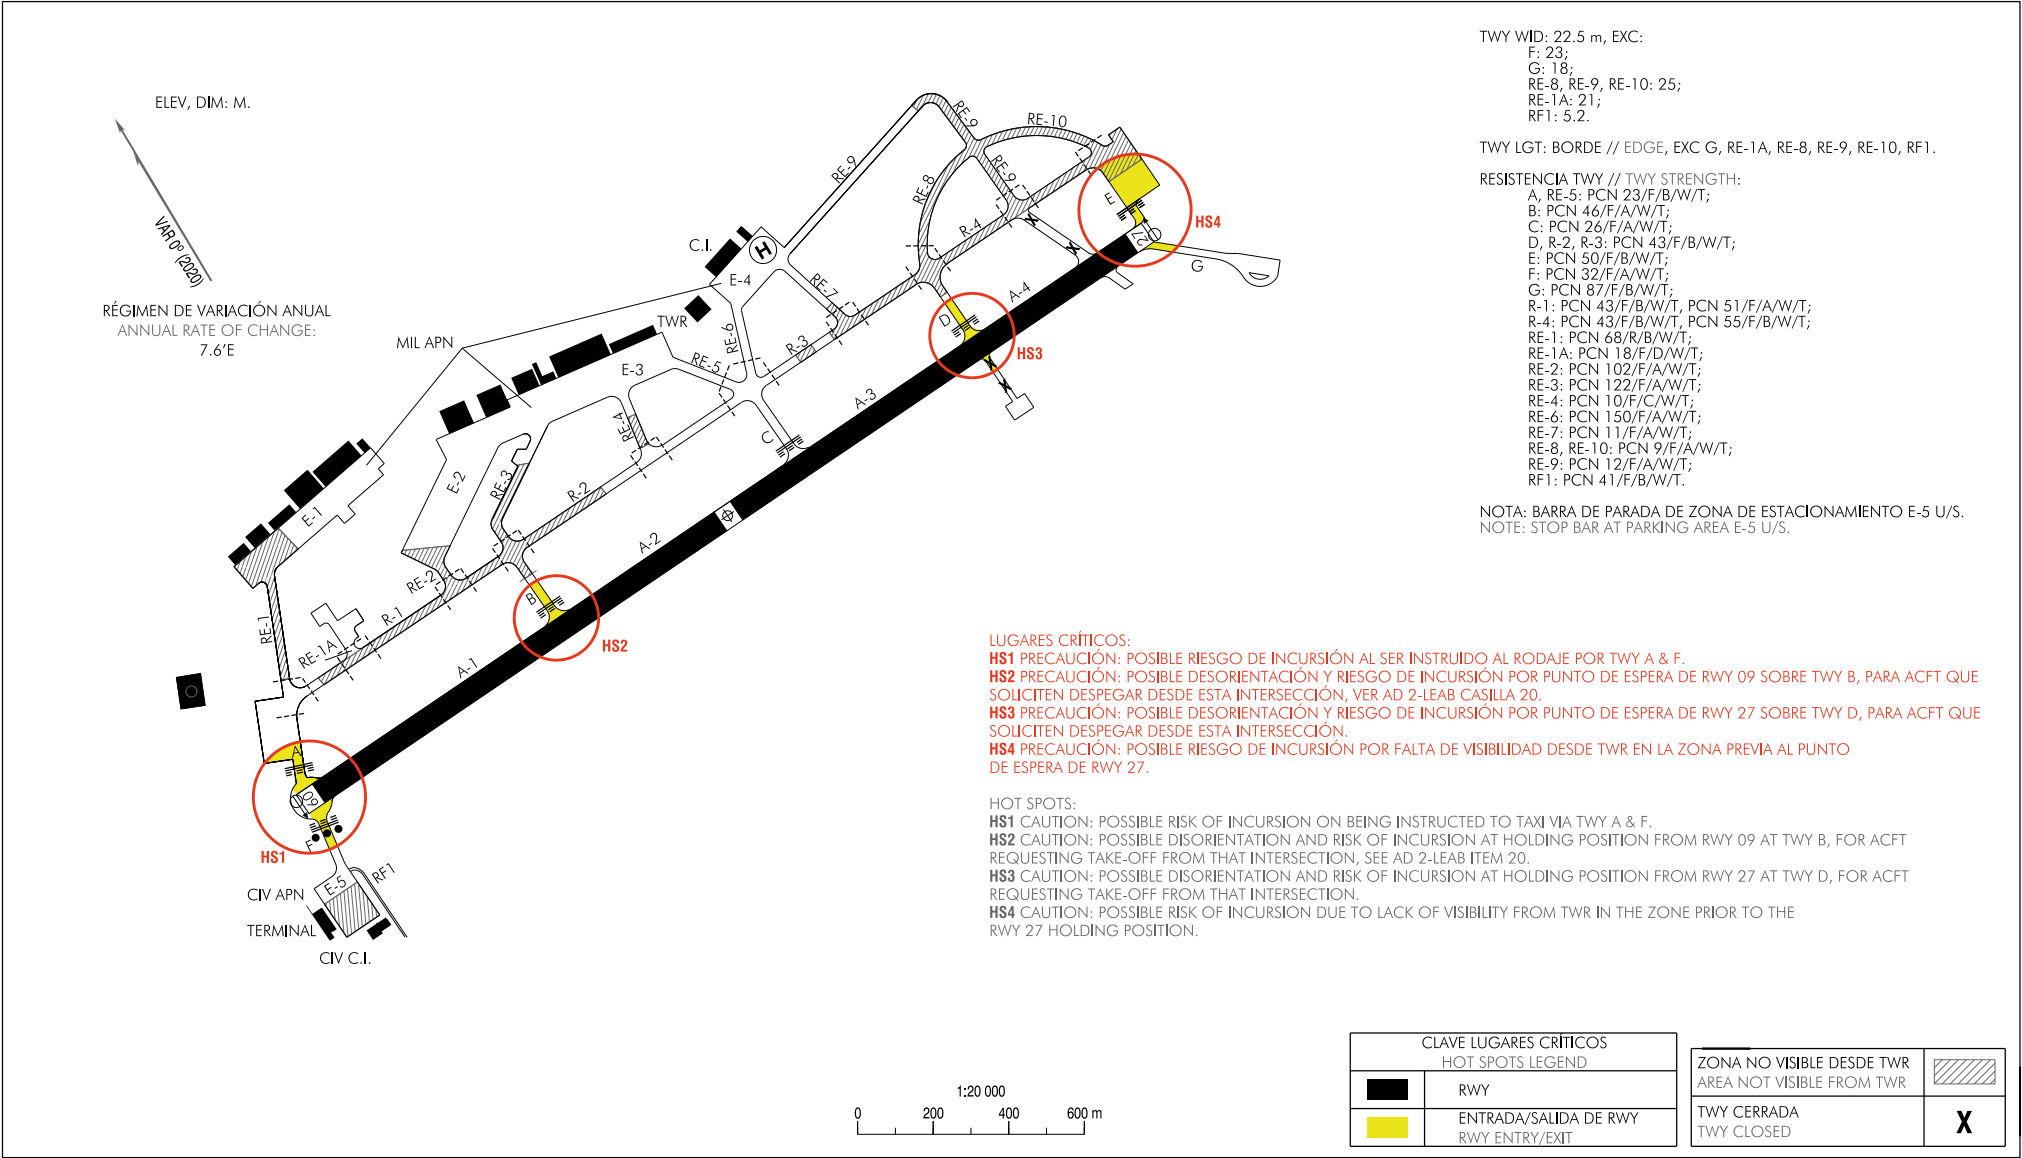


INTENCIONADAMENTE EN BLANCO
INTENTIONALLY BLANK

PLANO DE ESTACIONAMIENTO
Y ATRAQUE DE AERONAVES-OACI

ELEV
CIV APN
696 m

TWR 122.105 C
GND 121.805 C

ALBACETE

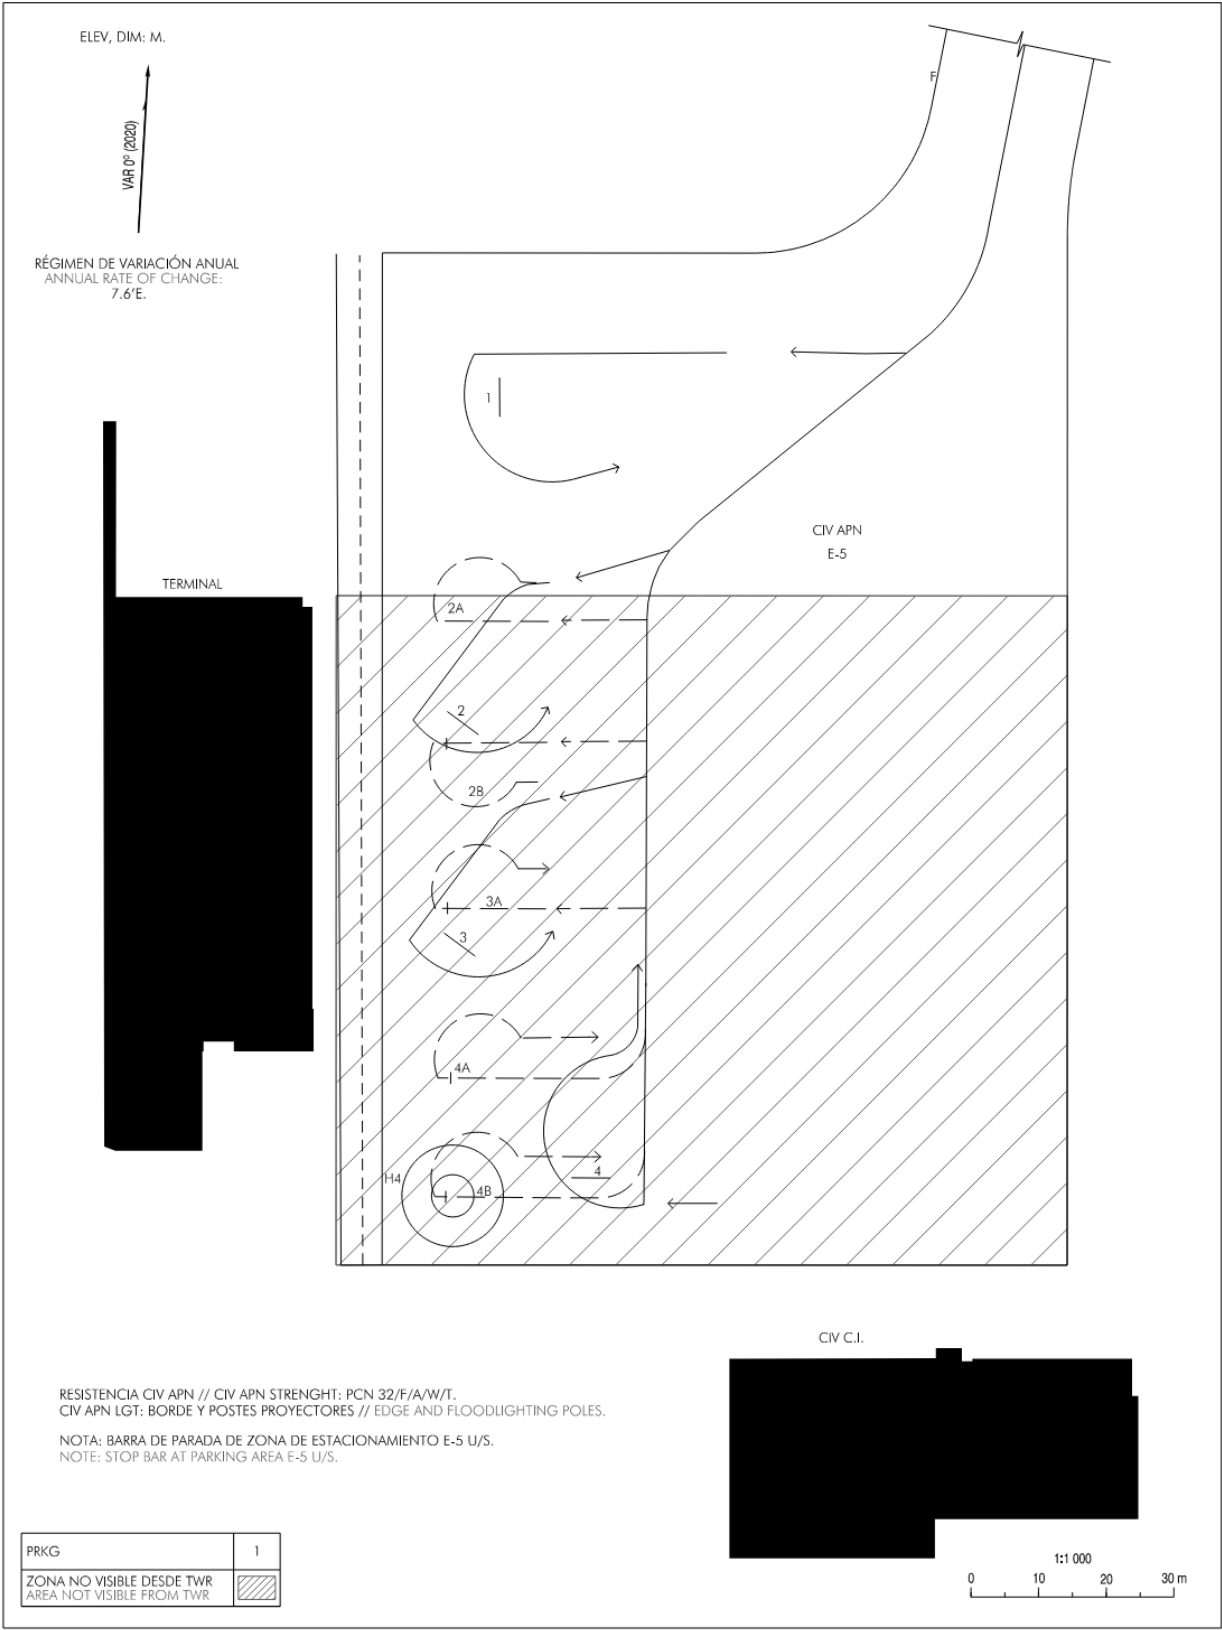

REIMPRESIÓN.
REPRINT.

CAMBIOS:
CHANGES:

CARACTERÍSTICAS DE LOS PUESTOS DE ESTACIONAMIENTO
AIRCRAFT STANDS CHARACTERISTICS

PRKG	RAMPA	COORD	SALIDA	MAX_ACFT	APROAR	OBSERVACIONES
PRKG	RAMP	COORD	EXIT	MAX_ACFT	NOSE_TO	REMARKS
1	-	385646.02N 0015247.28W	A	A320	-	(1)
2	-	385644.30N 0015247.73W	A	F900	-	INCOMP 2A, 2B (1)
2A	-	385644.69N 0015247.61W	A	C25A	-	INCOMP 2
2B	-	385644.08N 0015247.61W	A	C25A	-	INCOMP 2,3
3	-	385643.20N 0015247.70W	A	F900	-	INCOMP 2B, 3A (1)
3A	-	385643.26N 0015247.57W	A	C25A	-	INCOMP 3
4	-	385641.97N 0015246.25W	A	GLF4	-	INCOMP 4B, H4
4A	-	385642.42N 0015247.51W	A	C25A	-	INCOMP 4
4B	-	385641.83N 0015247.51W	A	C25A	-	INCOMP 4, H4
H4	-	385641.83N 0015247.47W	A	EC45	-	INCOMP 4, 4B (2)
Observaciones						
(1)	Durante la salida se debe interrumpir la circulación en el vial de servicio.					
(2)	Envergadura MAX: 13.03 m.					
Remarks						
(1)	All service road traffic must be halted during exits.					
(2)	MAX wingspan: 13.03 m.					