


CARTE D'AERODROME
Aerodrome chart

ATIS : DE GAULLE 128.230 (FR) ☎ 01 48 62 10 92 - 127.130 (EN)
DELIVERY (PREVOL) : 121.840 - 121.730
GND (SOL) : 121.610 - 121.810 - 121.980 - 121.780
ATS : H24

PARIS CHARLES DE GAULLE
49 00 35 N - 002 32 52 E
ALT AD : 392 (15 hPa)

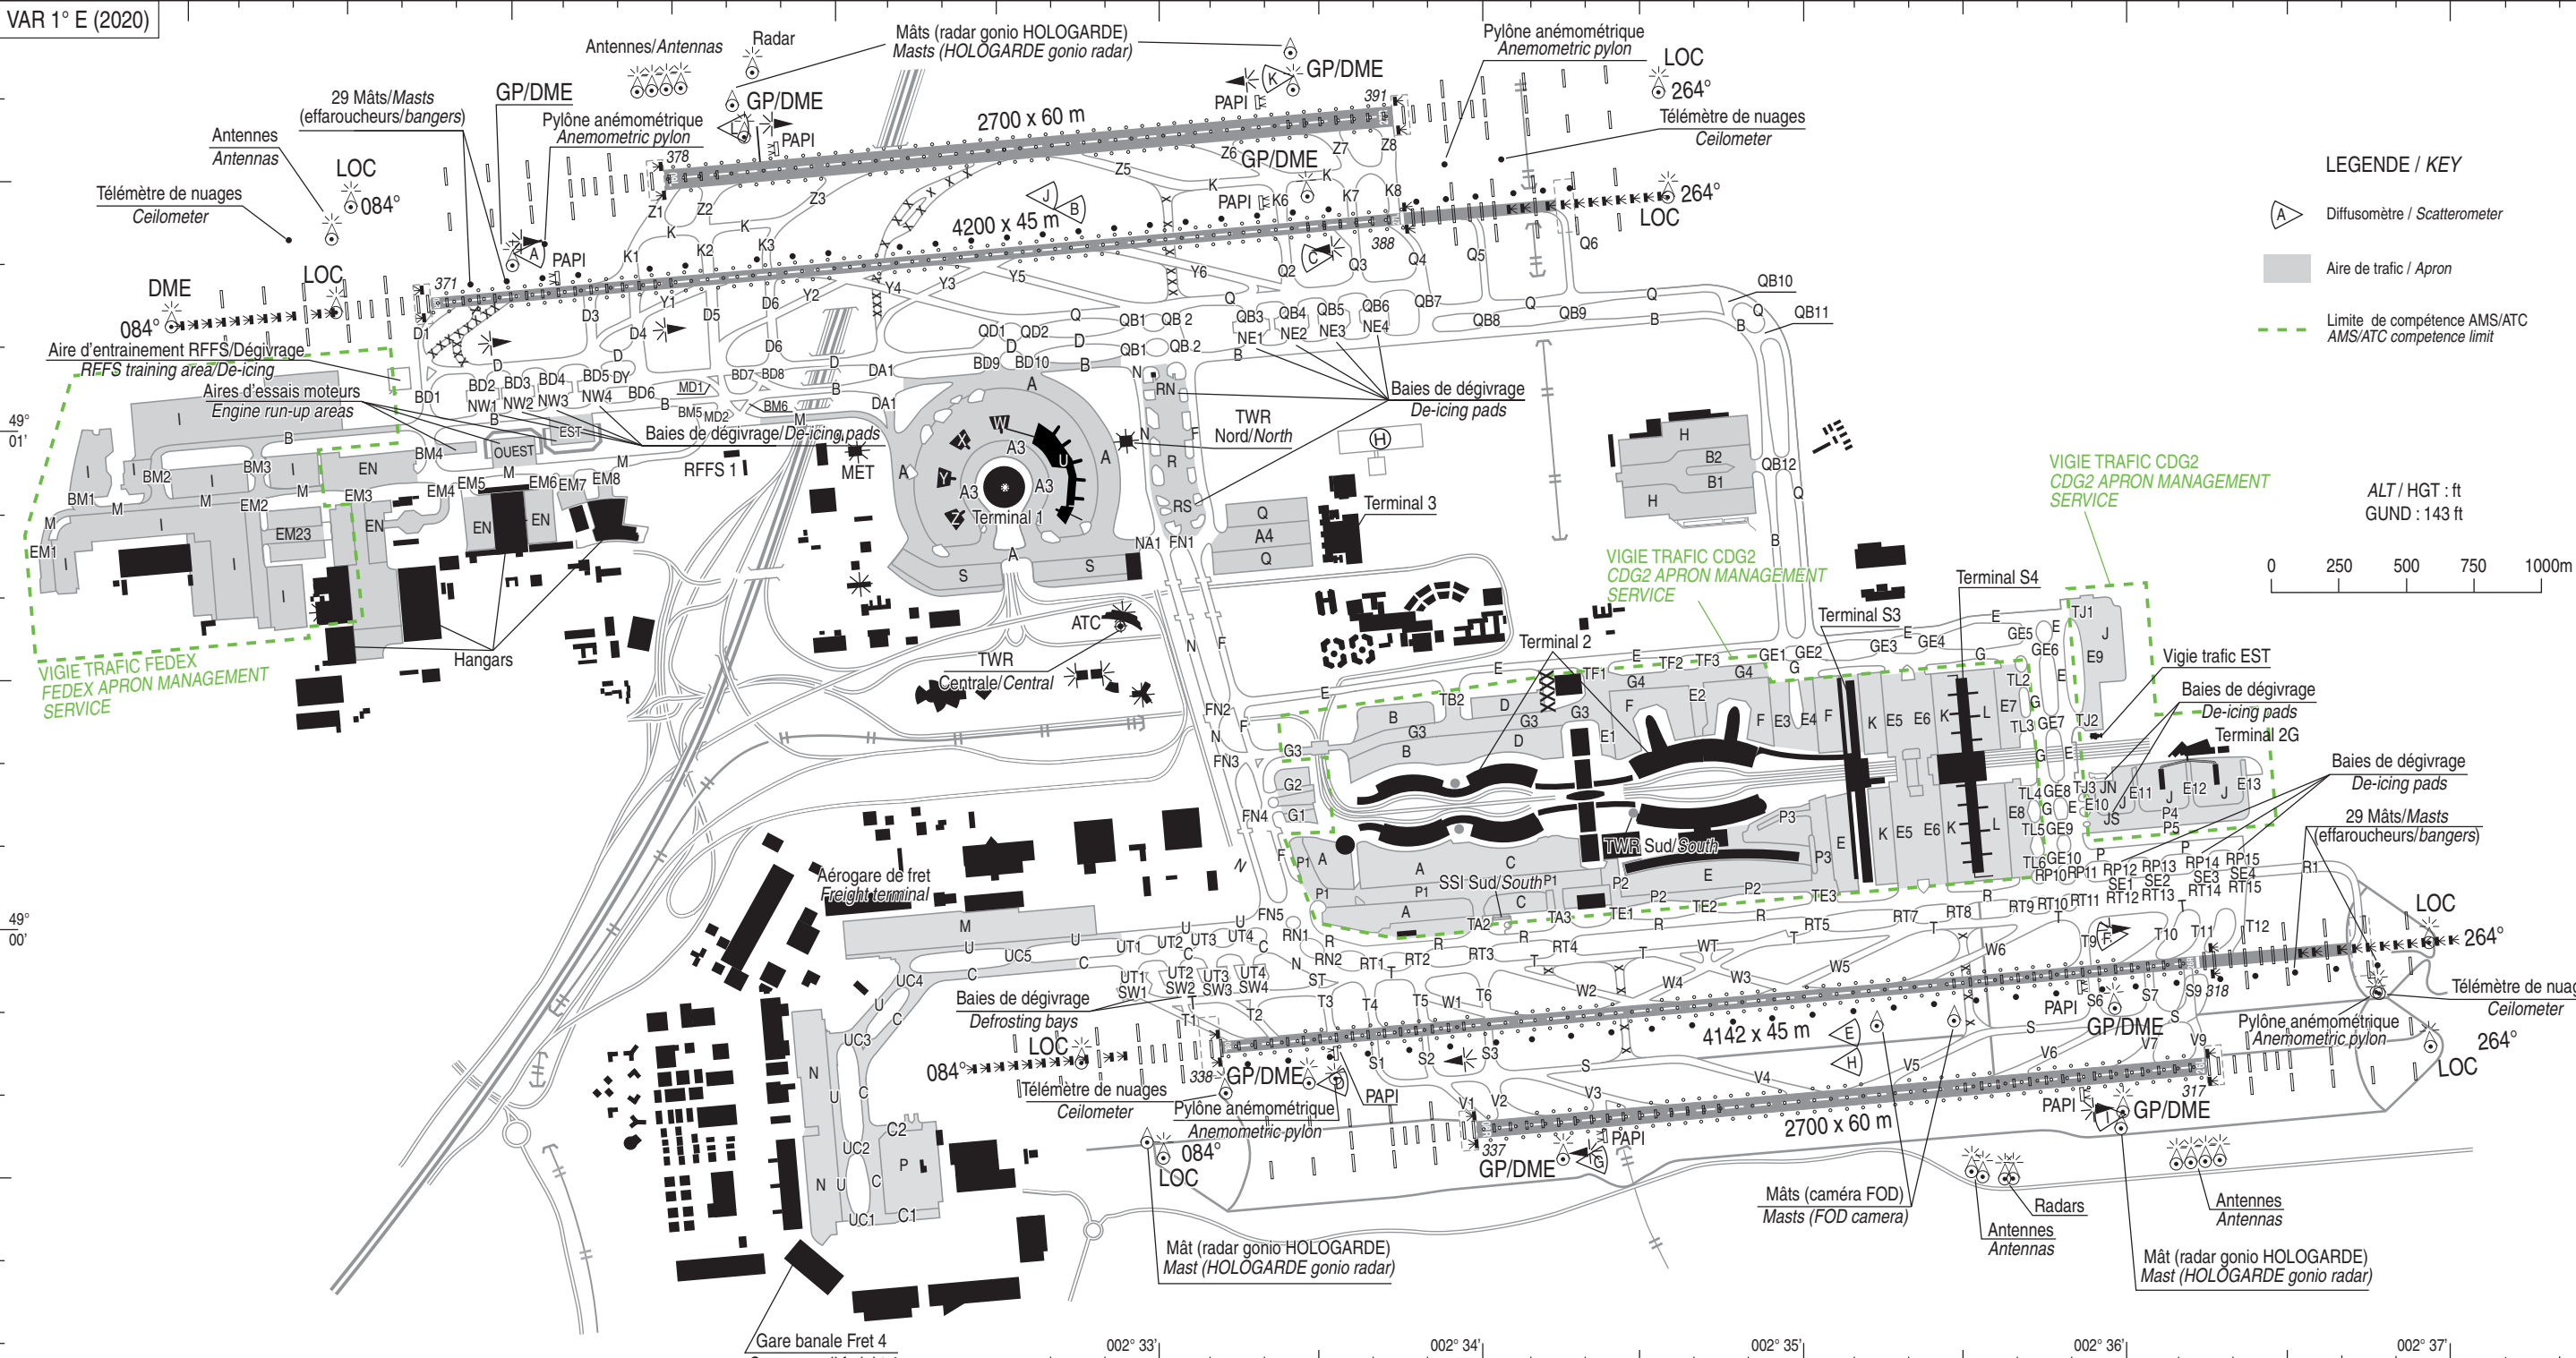

LEGENDE / KEY

- Diffusomètre / Scatterometer
- Aire de trafic / Apron
- Limite de compétence AMS/ATC
AMS/ATC competence limit

ALT / HGT : ft
GUND : 143 ft

0 250 500 750 1000m

ATTENTION PARTICULIERE / CAUTION :

(1) Voir/See AD 2 LFPG.12
(2) Voir/See AD 2 LFPG.13

Etre très attentif aux clairances de traversée de piste.
Le collationnement de toute instruction d'attente avant une traversée de piste est exigé.
Strictly follow RWY crossing clearance.
It is mandatory to read back all holding instructions before a RWY crossing.

Marques de points d'attente / Holding points marks : voir/see AD 2 LFPG ADC 02


COORDONNEES SEUILS / THR coordinates			RWY	BALISAGE/Lighting		TORA	TODA	ASDA	LDA	NATURE Surface	RESIST. Strength	MINIMUM TKOF (RVR : m)			
TYPE	LATITUDE	LONGITUDE		APCH	RWY							CAT A	CAT B	CAT C	CAT D
THR 09L	49° 01' 28.99" N	002° 31' 29.62" E	09L	LIH-LED 900m	LIH-LED	2700	2760	2700	2700	Revêtements Paved	100 F/B/W/T	150	150	150	200
THR 27R	49° 01' 36.10" N	002° 33' 42.09" E	27R	LIH-LED 900m	LIH-LED	2700	2760	2700	2700			150	150	150	200
THR 09R	49° 01' 14.22" N	002° 30' 47.01" E	09R	LIH-LED 900m	LIH-LED	4200(2)	4260	4200	4200		100 R/B/W/T(1)	150	150	150	200
THR 27L	49° 01' 25.29" N	002° 34' 13.06" E	27L	LIH-LED 900m	LIH-LED	4200(2)	4260	4200	3600			150	150	150	200
DTHR 27L	49° 01' 23.71" N	002° 33' 43.62" E	08L	LIH-LED 900m	LIH-LED	4142(2)	4202	4142	4142		100 R/B/W/T(1)	150	150	150	200
THR 08L	48° 59' 44.47" N	002° 33' 09.88" E	26R	LIH-LED 900m	LIH-LED	4142(2)	4202	4142	3616			150	150	150	200
THR 26R	48° 59' 55.32" N	002° 36' 32.99" E	08R	LIH-LED 900m	LIH-LED	2700	2760	2700	2700	100 R/B/W/T	100 R/B/W/T	150	150	150	200
DTHR 26R	48° 59' 53.95" N	002° 36' 07.24" E	26L	LIH-LED 900m	LIH-LED	2700	2760	2700	2700			150	150	150	200
THR 08R	48° 59' 34.49" N	002° 33' 56.38" E										150	150	150	200
THR 26L	48° 59' 41.56" N	002° 36' 08.77" E										150	150	150	200

Décollages par faible visibilité (LVTO) autorisés toutes RWY par RVR ≥ 75m.
TKOF with LVTO : authorized for all RWY with RVR ≥ 75m.

AIRE DE STATIONNEMENT

Parking areas
AEROGARE 1
Terminal 1

PARIS CHARLES DE GAULLE

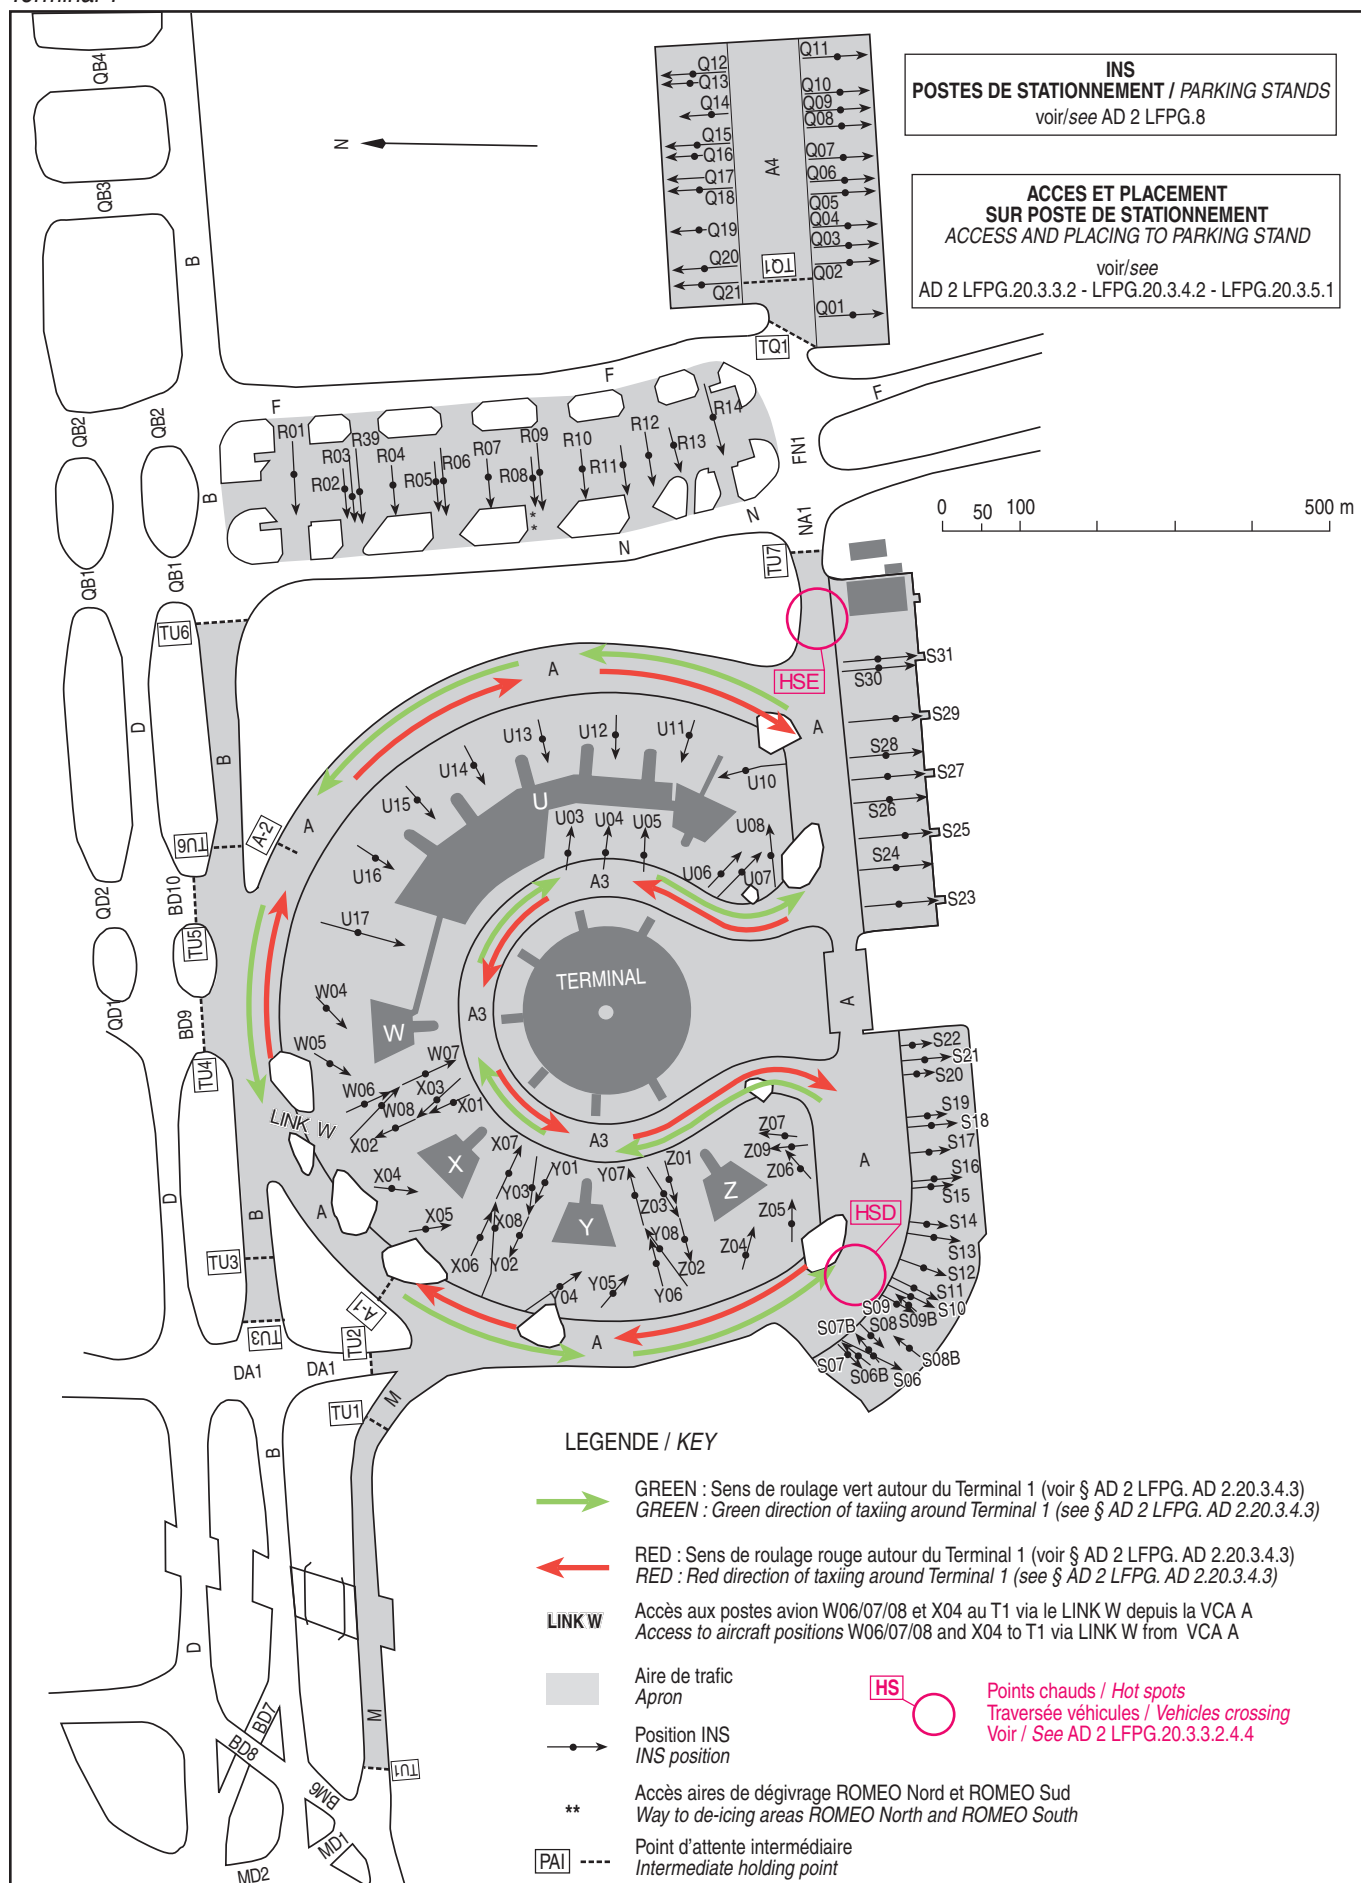


AIRES DE STATIONNEMENT

Parking areas


ALPHA - BRAVO - CHARLIE - DELTA - ECHO - FOX - GOLF - HOTEL

PARIS CHARLES DE GAULLE

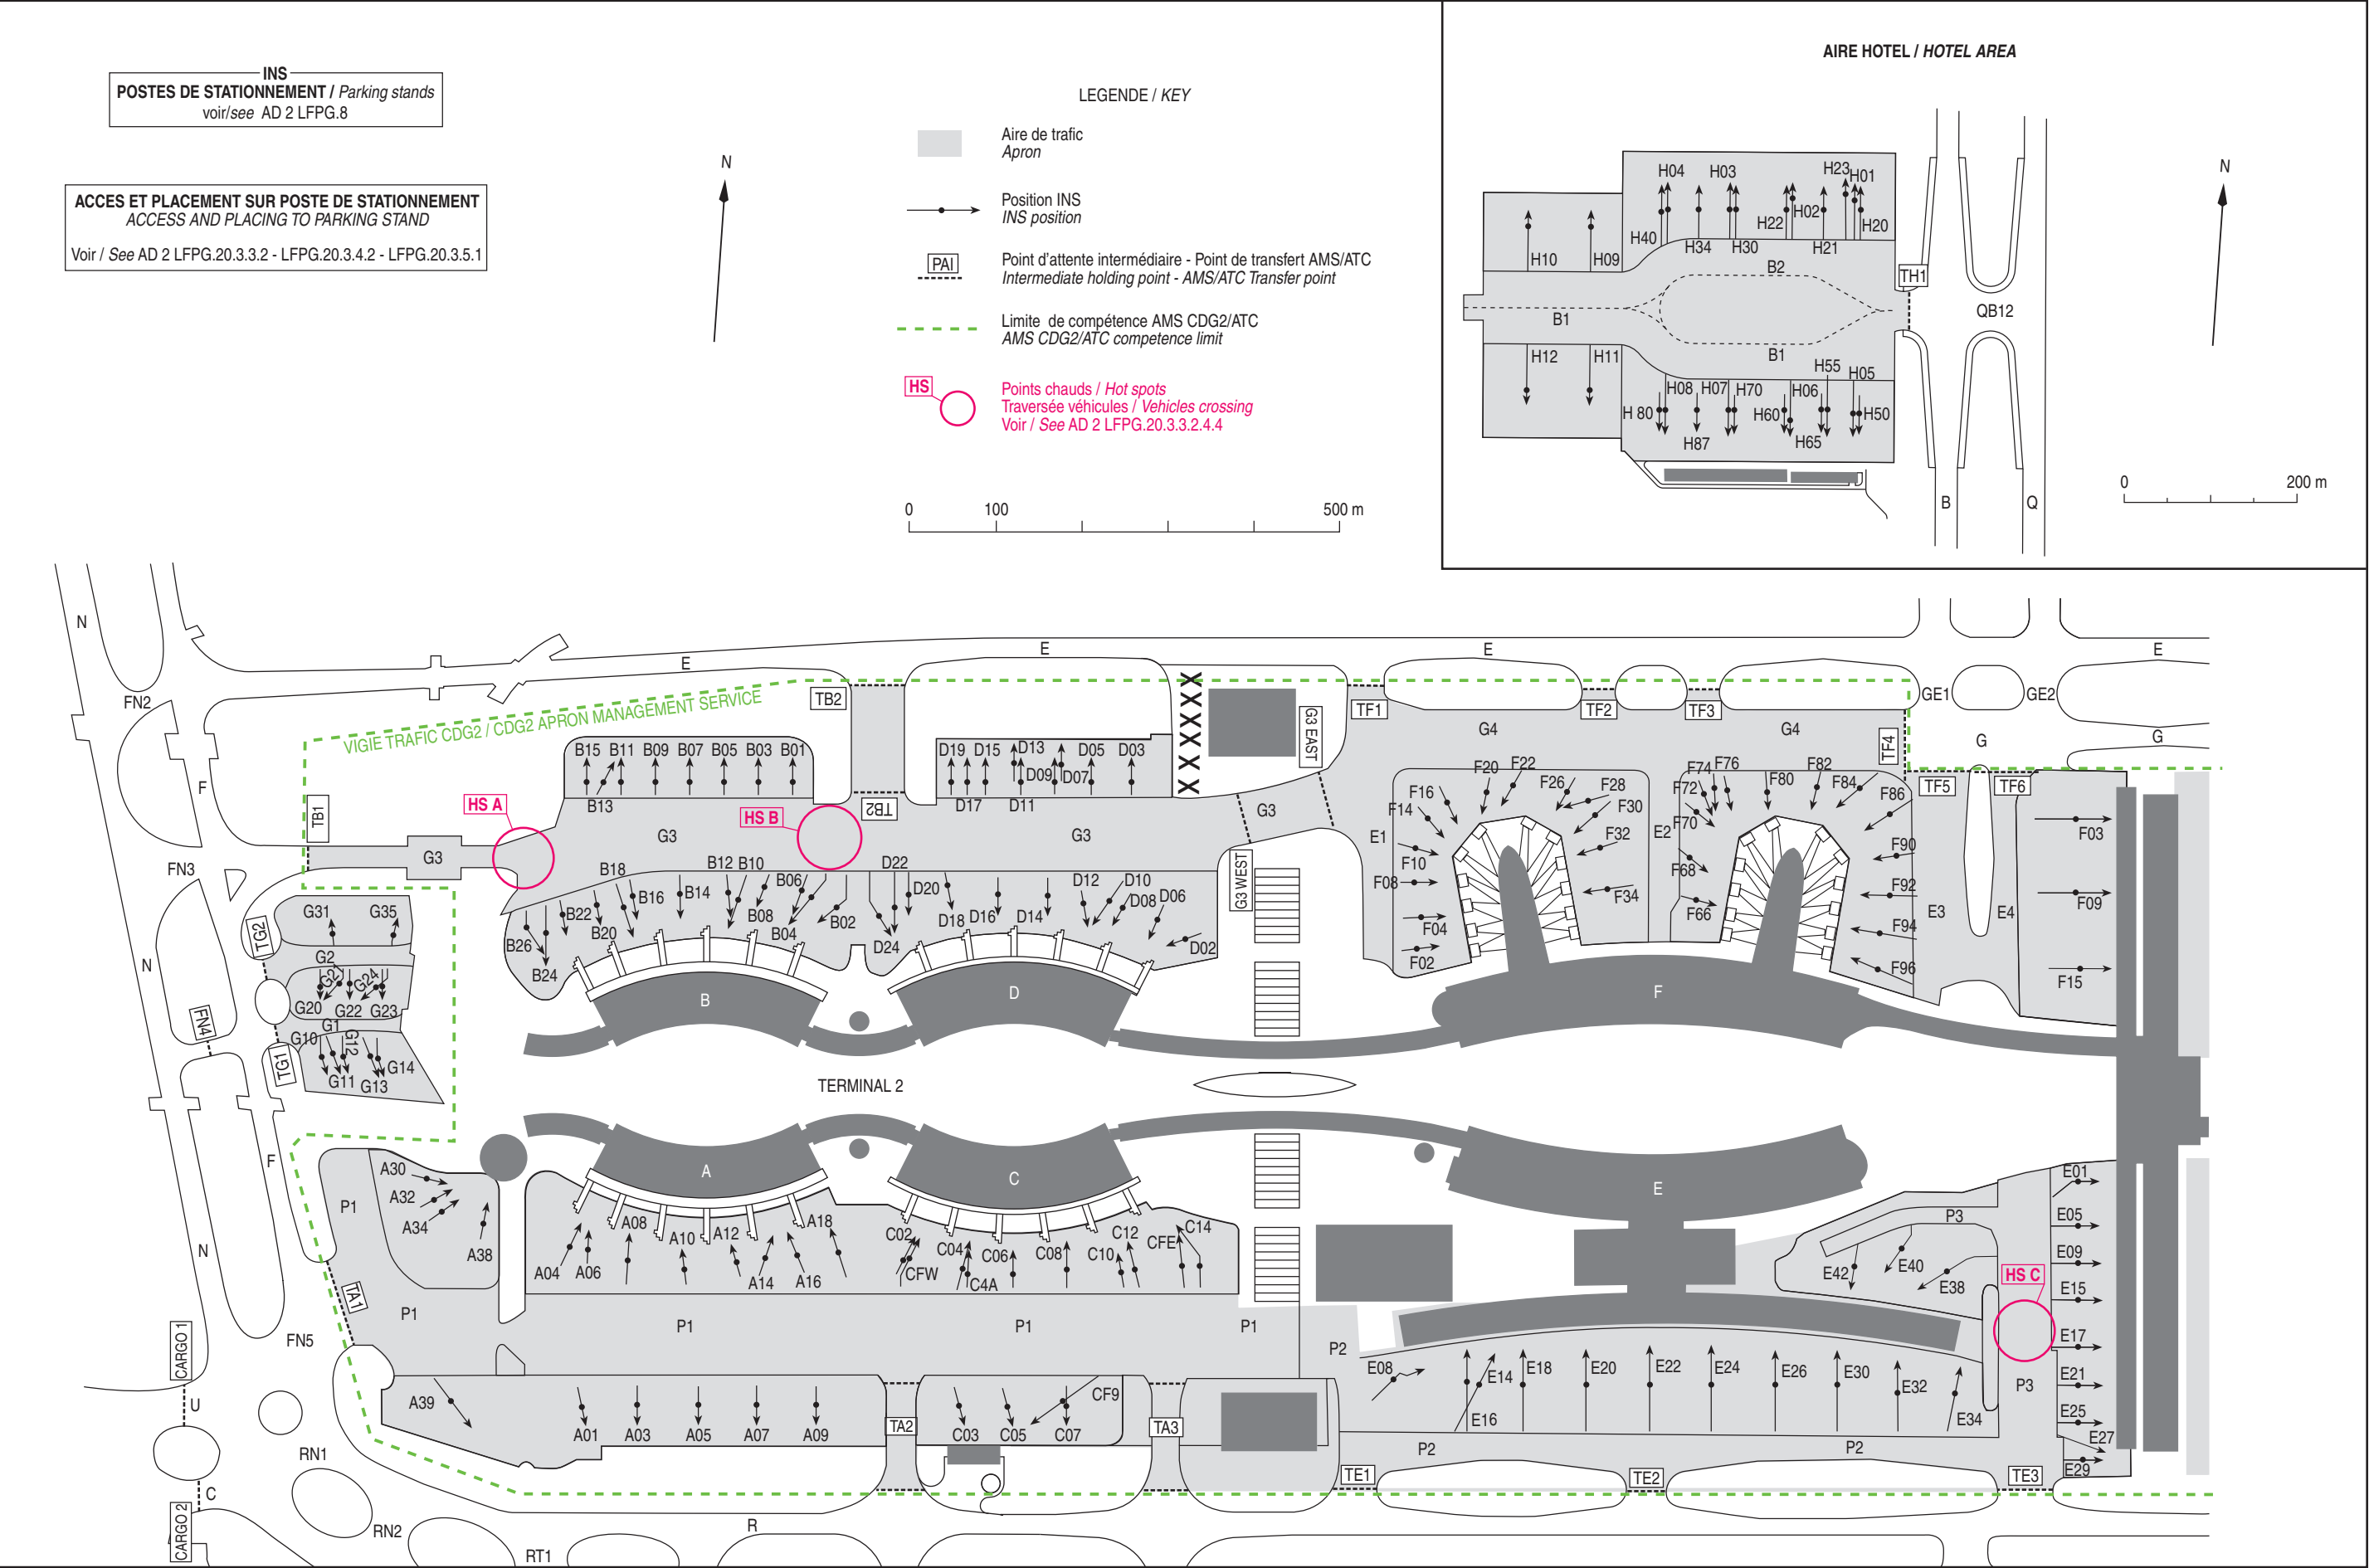

AIRES DE STATIONNEMENT
Parking areas
JULIETT - KILO - LIMA

PARIS CHARLES DE GAULLE

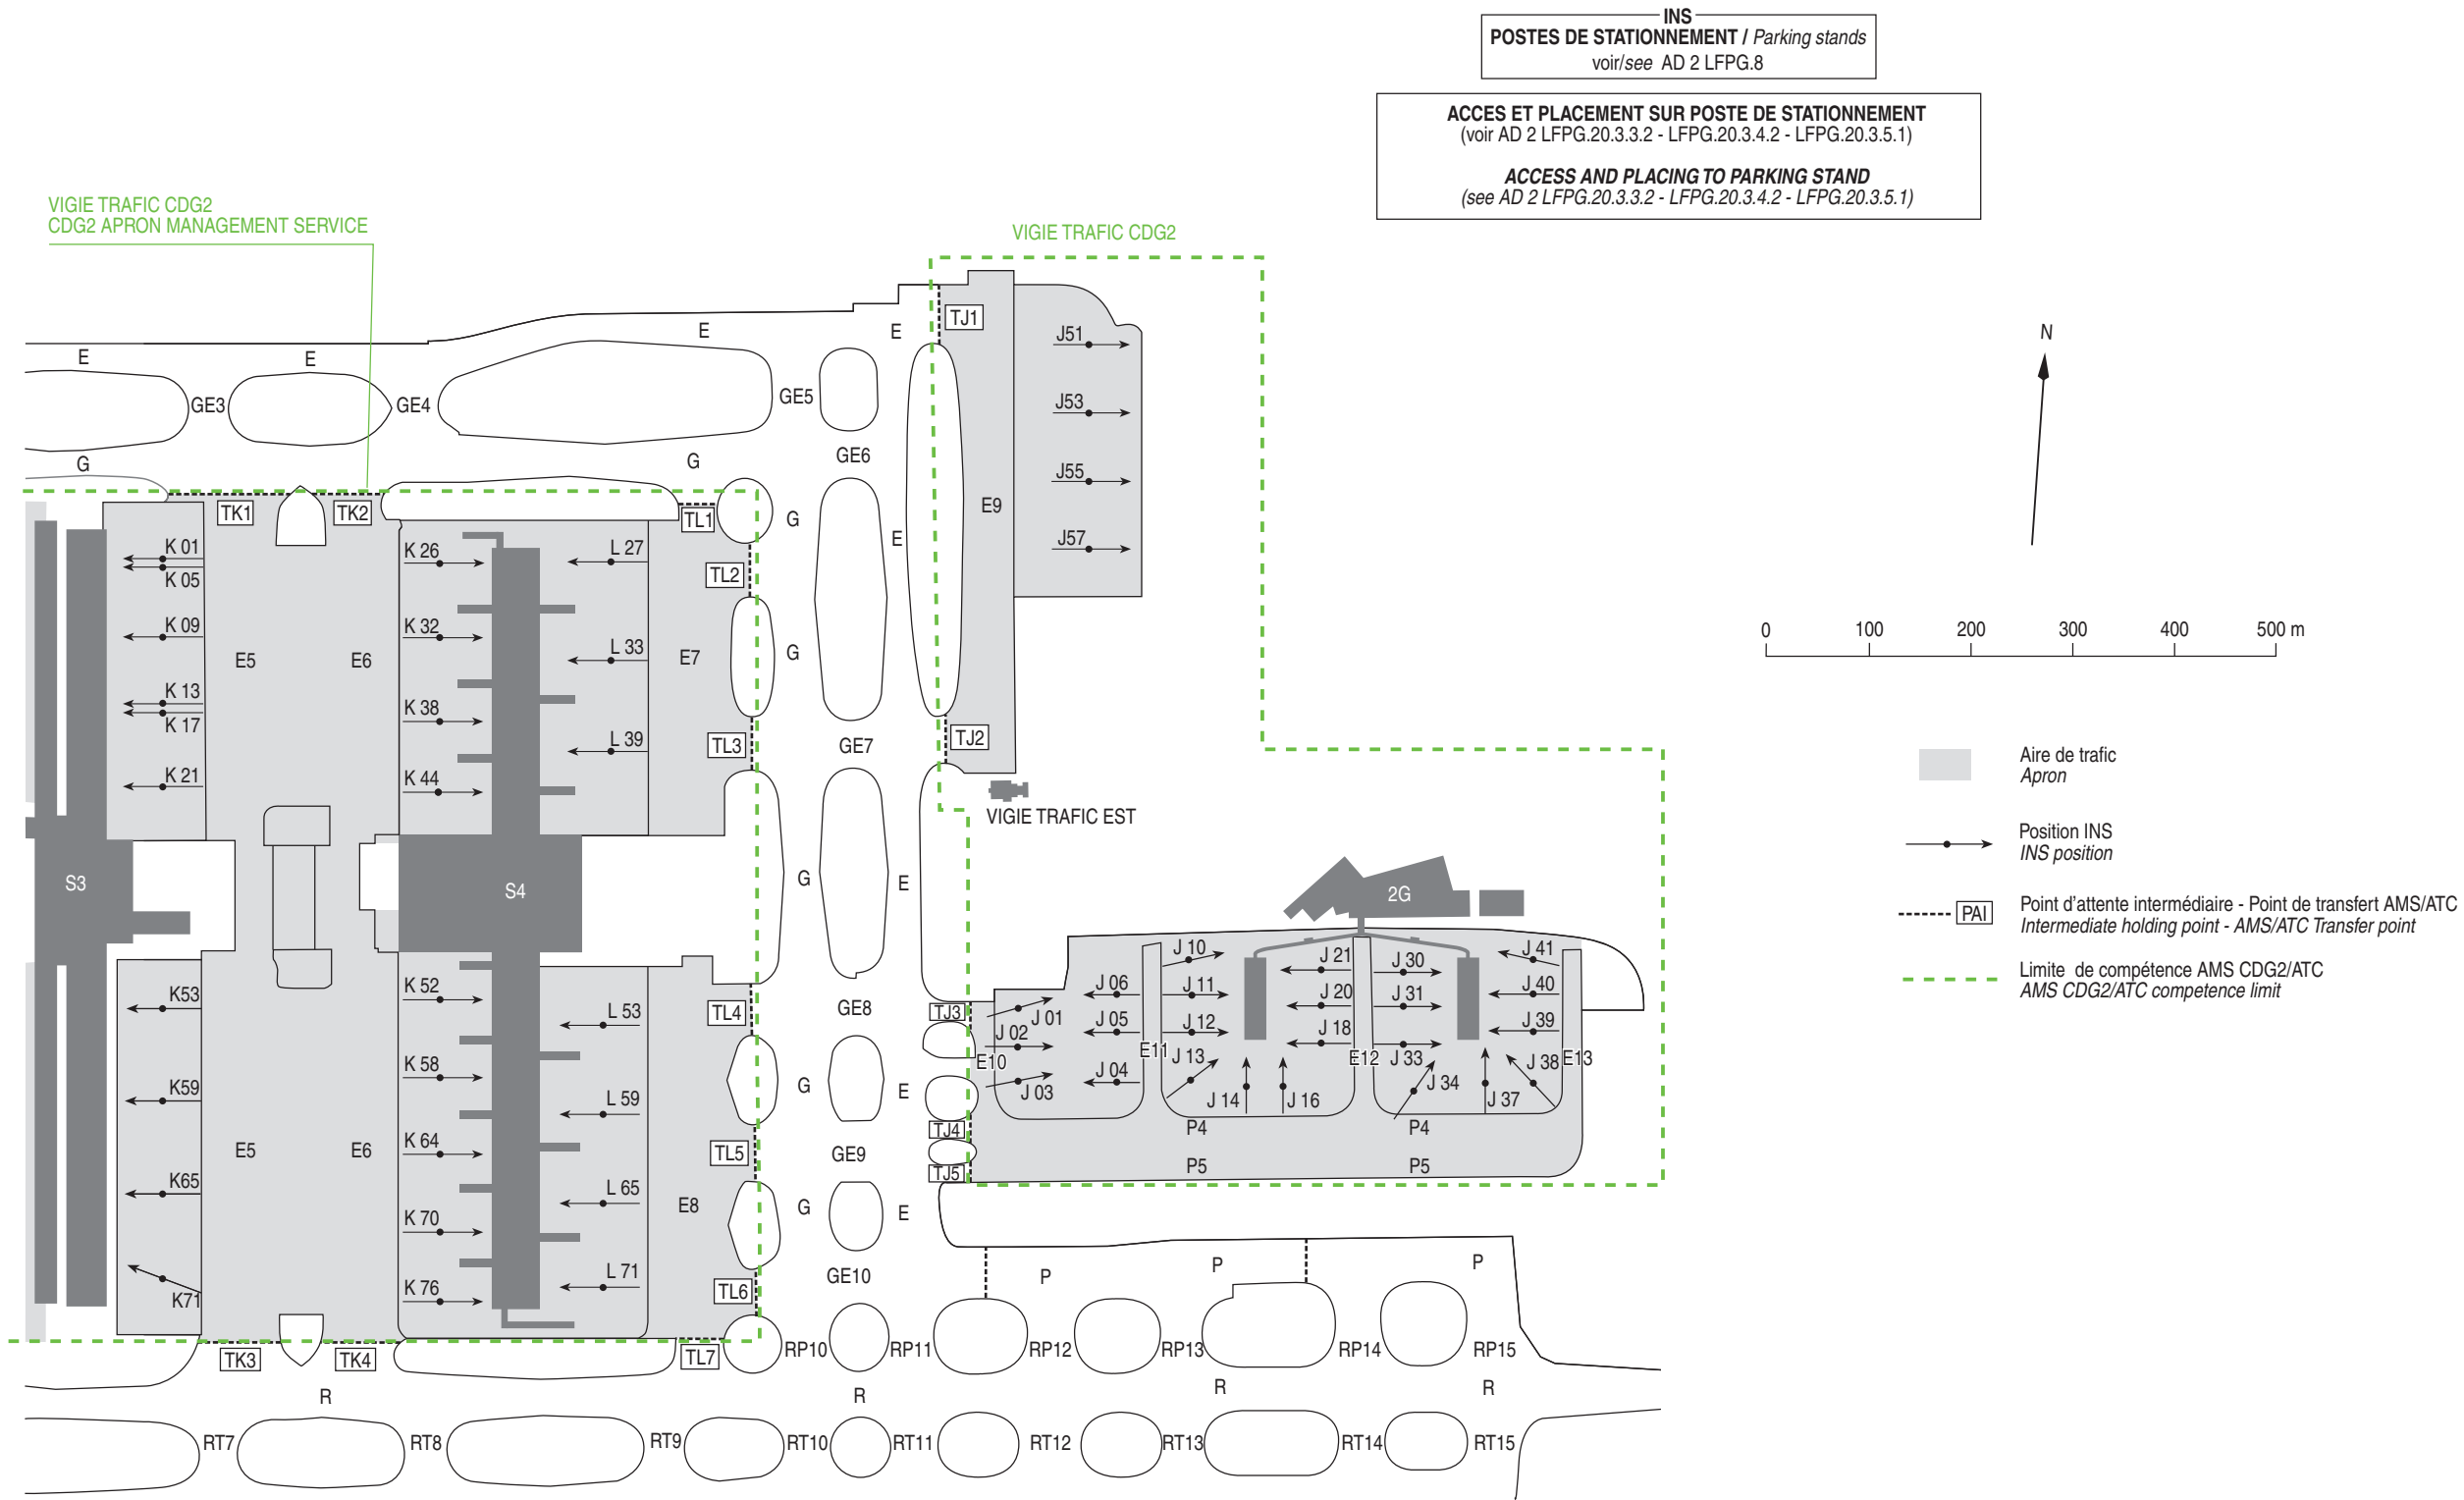


AIRES DE STATIONNEMENT

Parking areas

ECHO NOVEMBRE - INDIA

PARIS CHARLES DE GAULLE

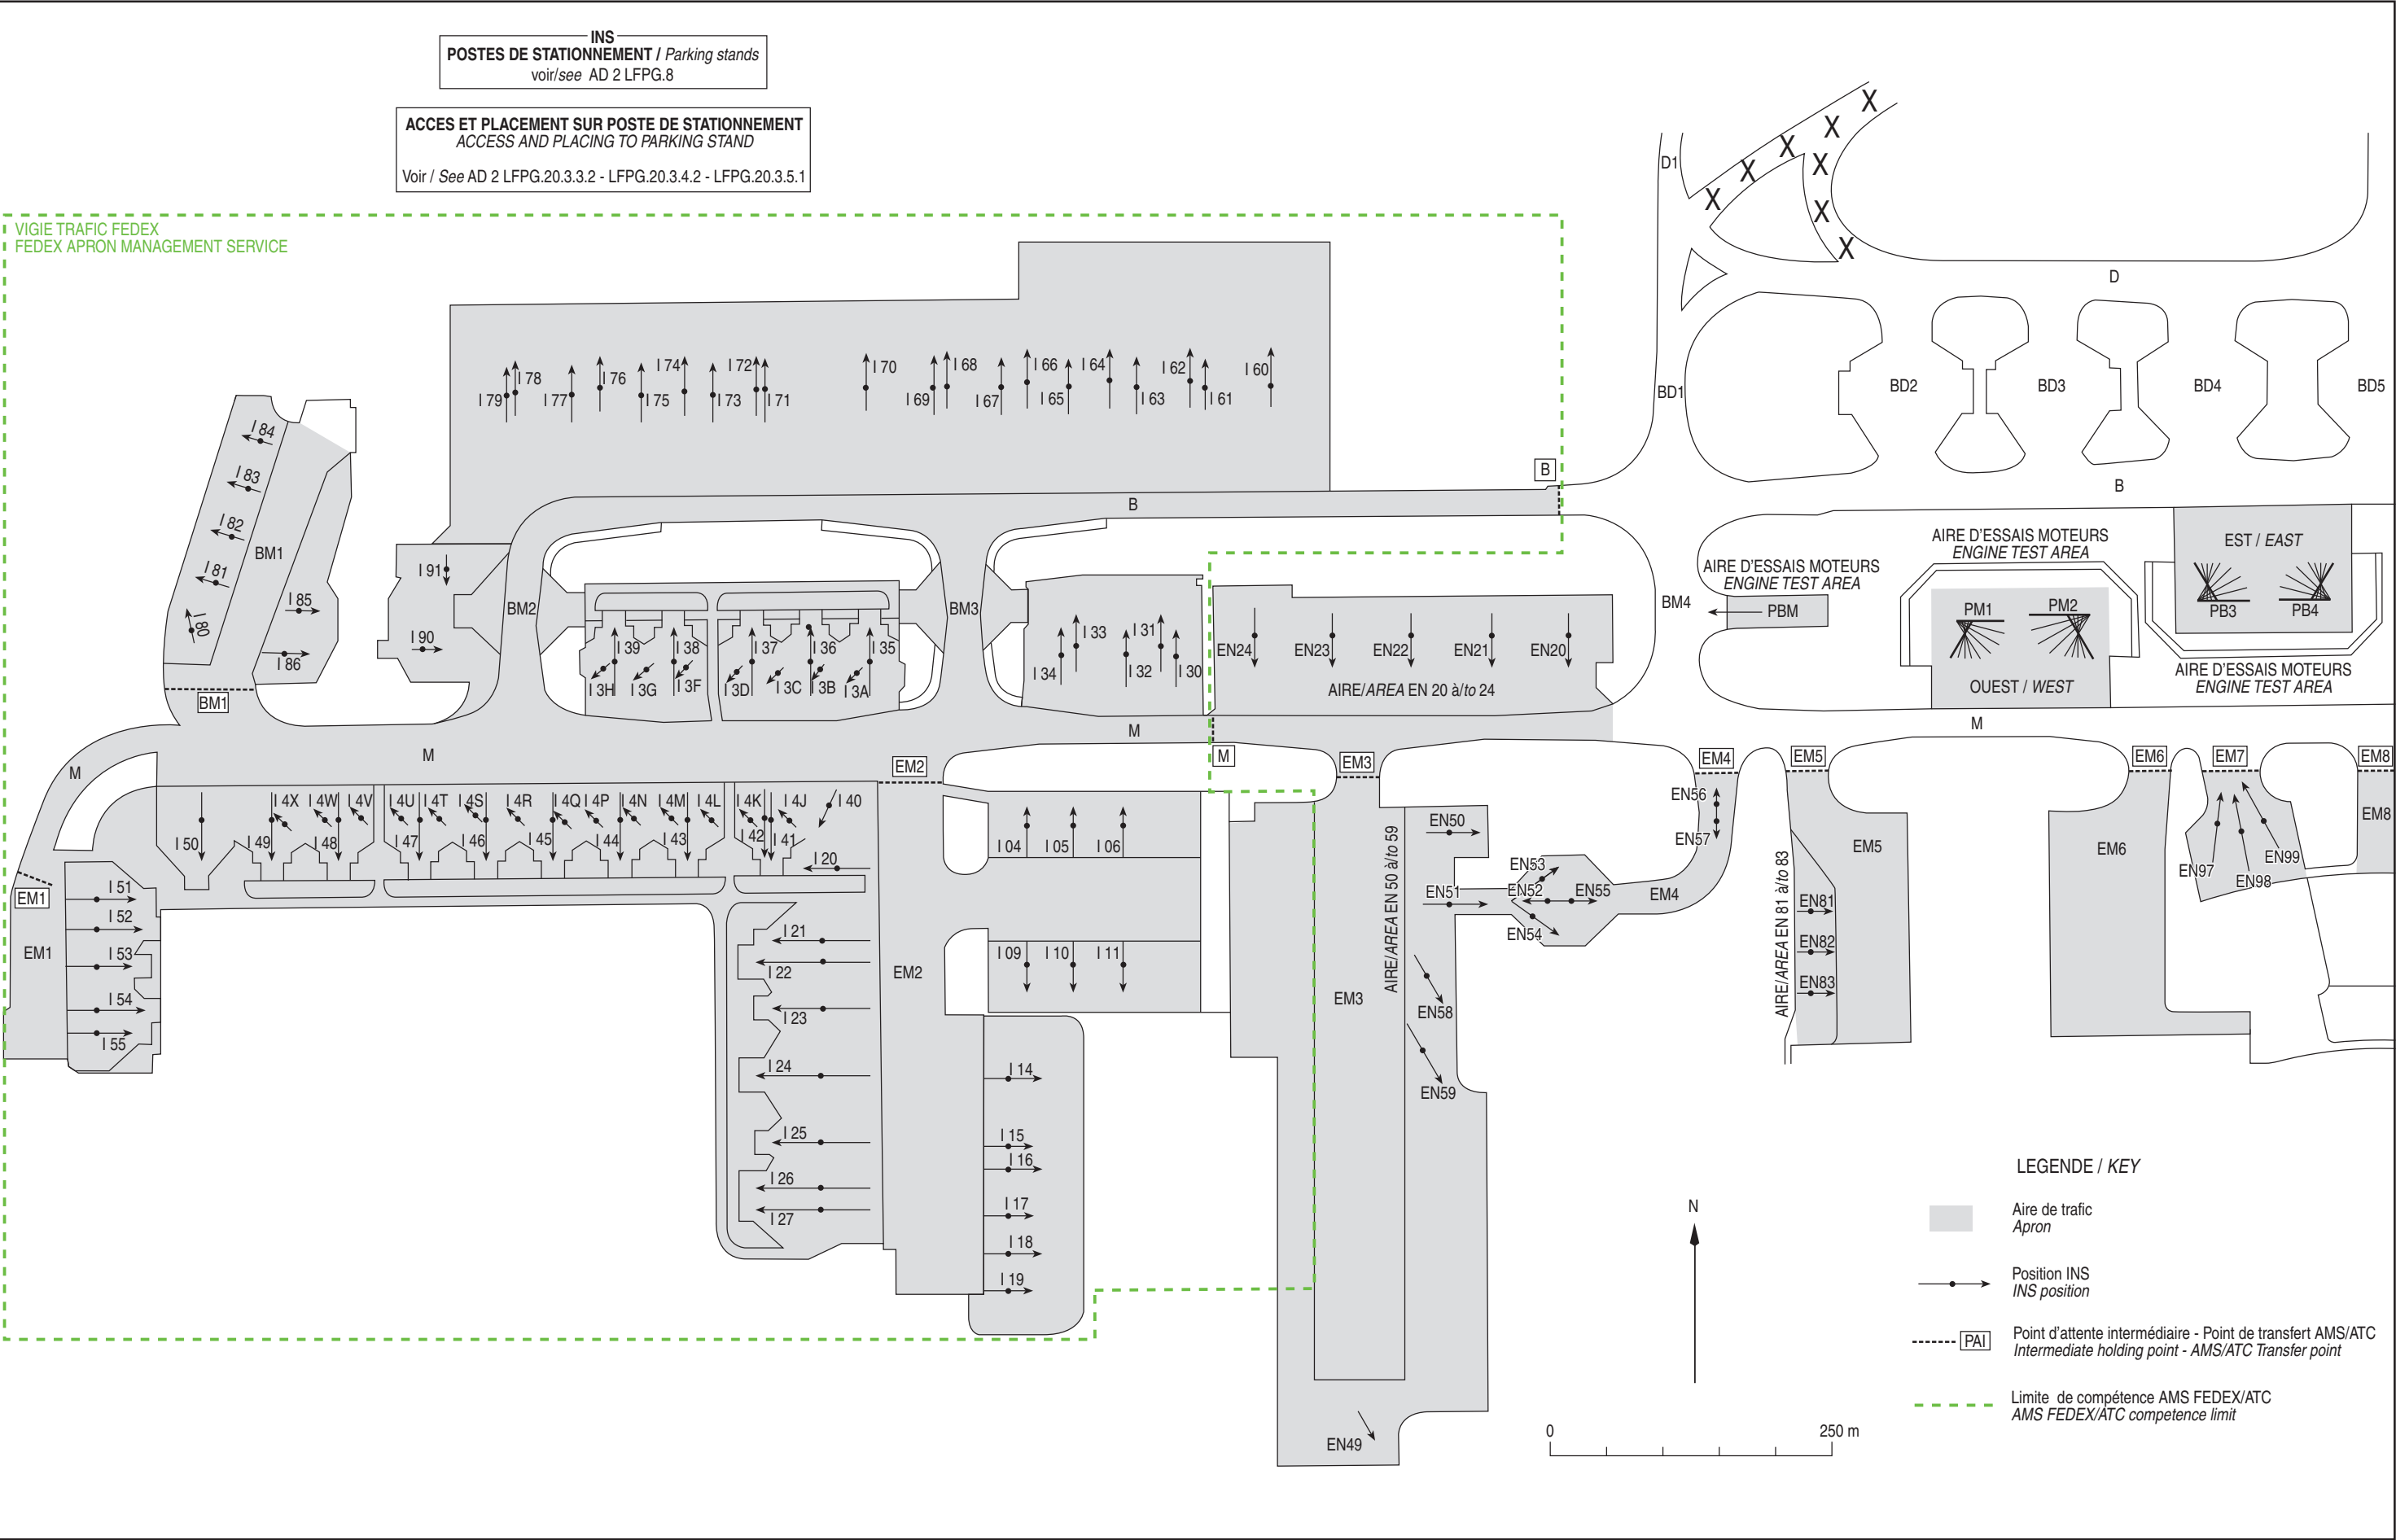

AIRE DE STATIONNEMENT

Parking areas

ZONE DE FRET

Freight zone

PARIS CHARLES DE GAULLE

