


PLANO DE AERÓDROMO-OACI

431807N  
0082238W

ELEV 101 m

TWR 118.305 C  
GMC 121.705 C

A CORUÑA

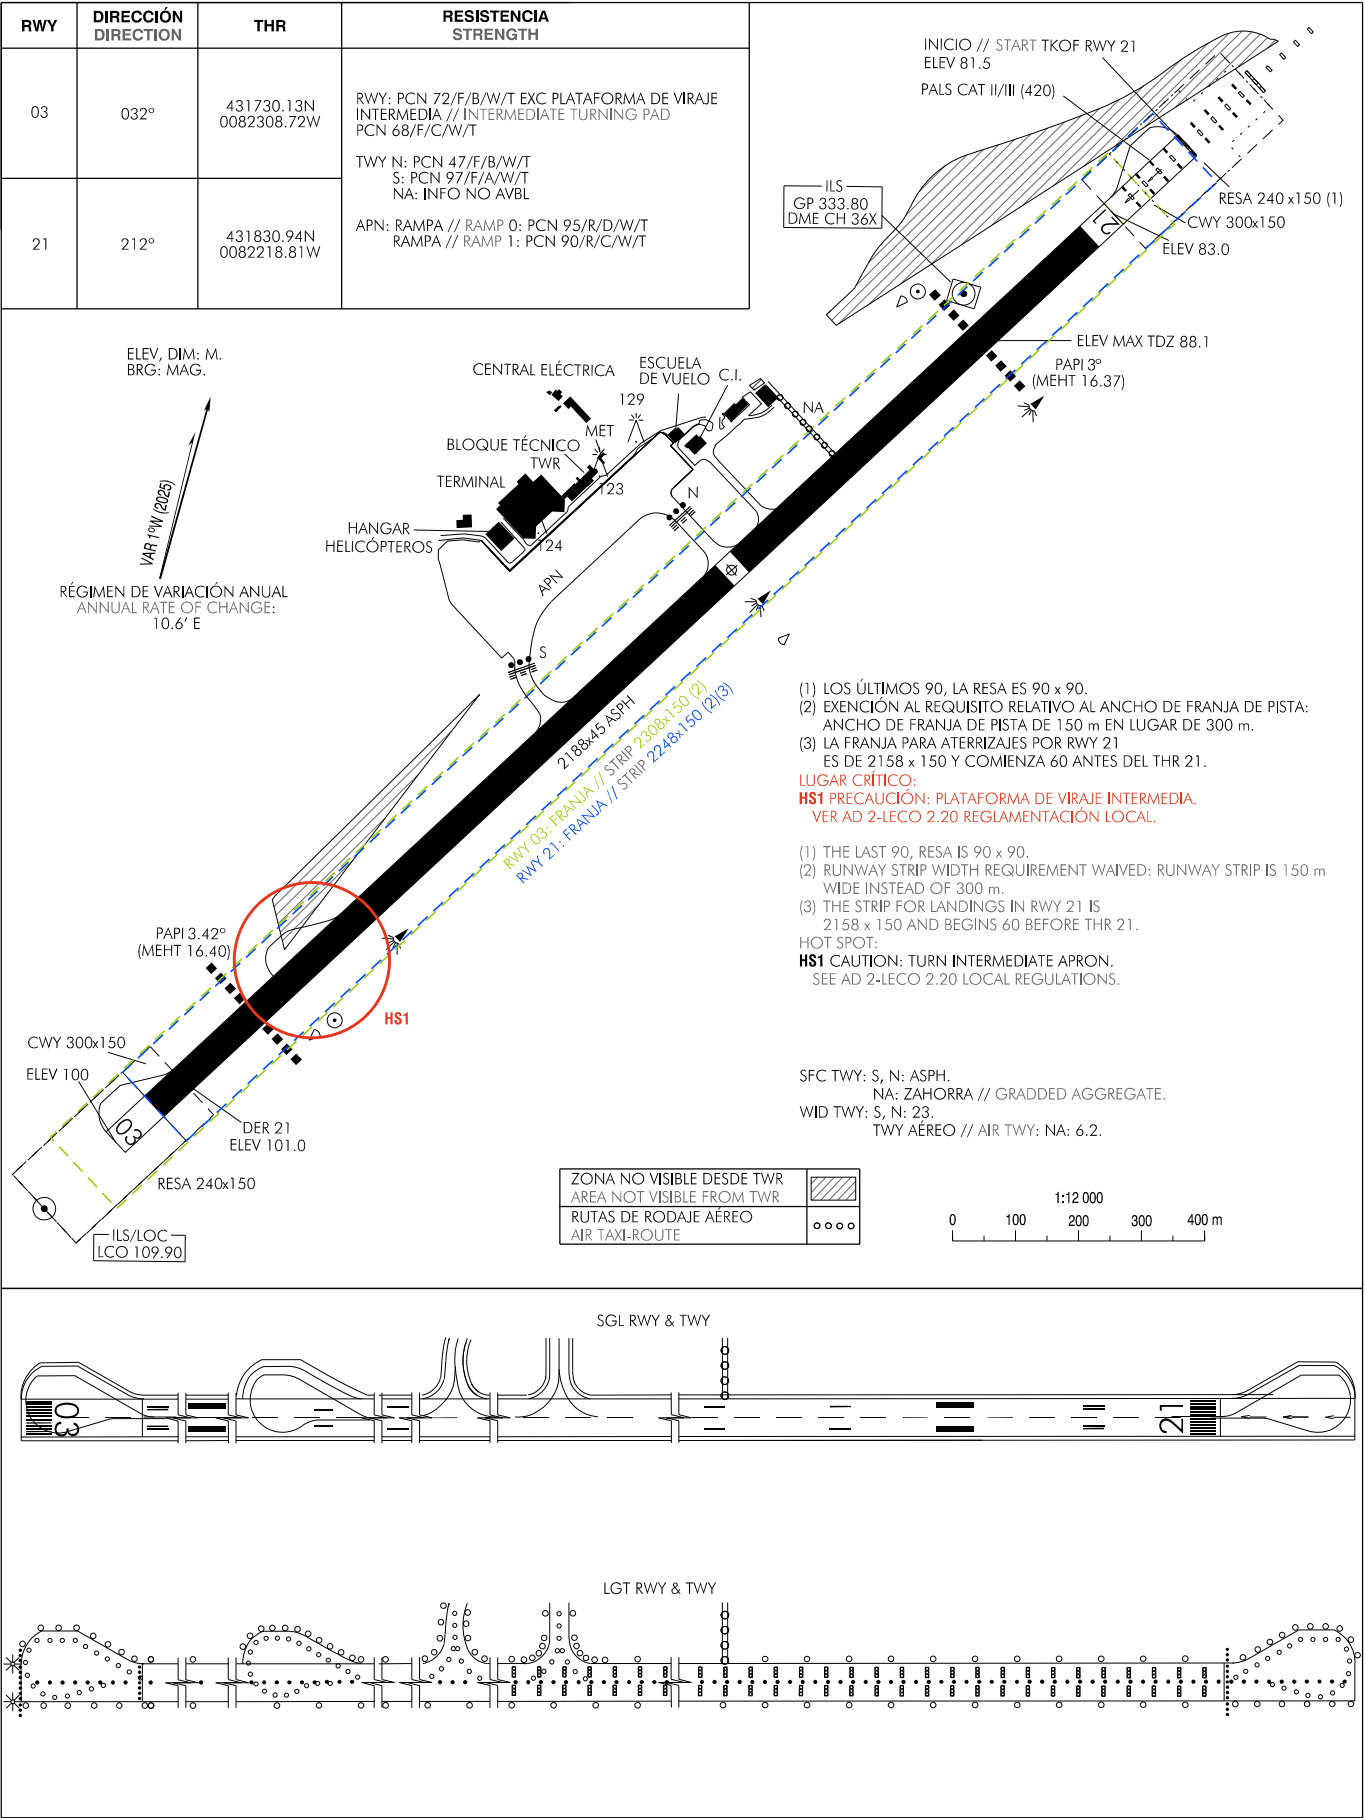


**INTENCIONADAMENTE EN BLANCO**  
**INTENTIONALLY BLANK**

PLANO DE ESTACIONAMIENTO  
Y ATRAQUE DE AERONAVES-OACI

ELEV APN  
93 m

TWR 118.305 C  
GMC 121.705 C

A CORUÑA

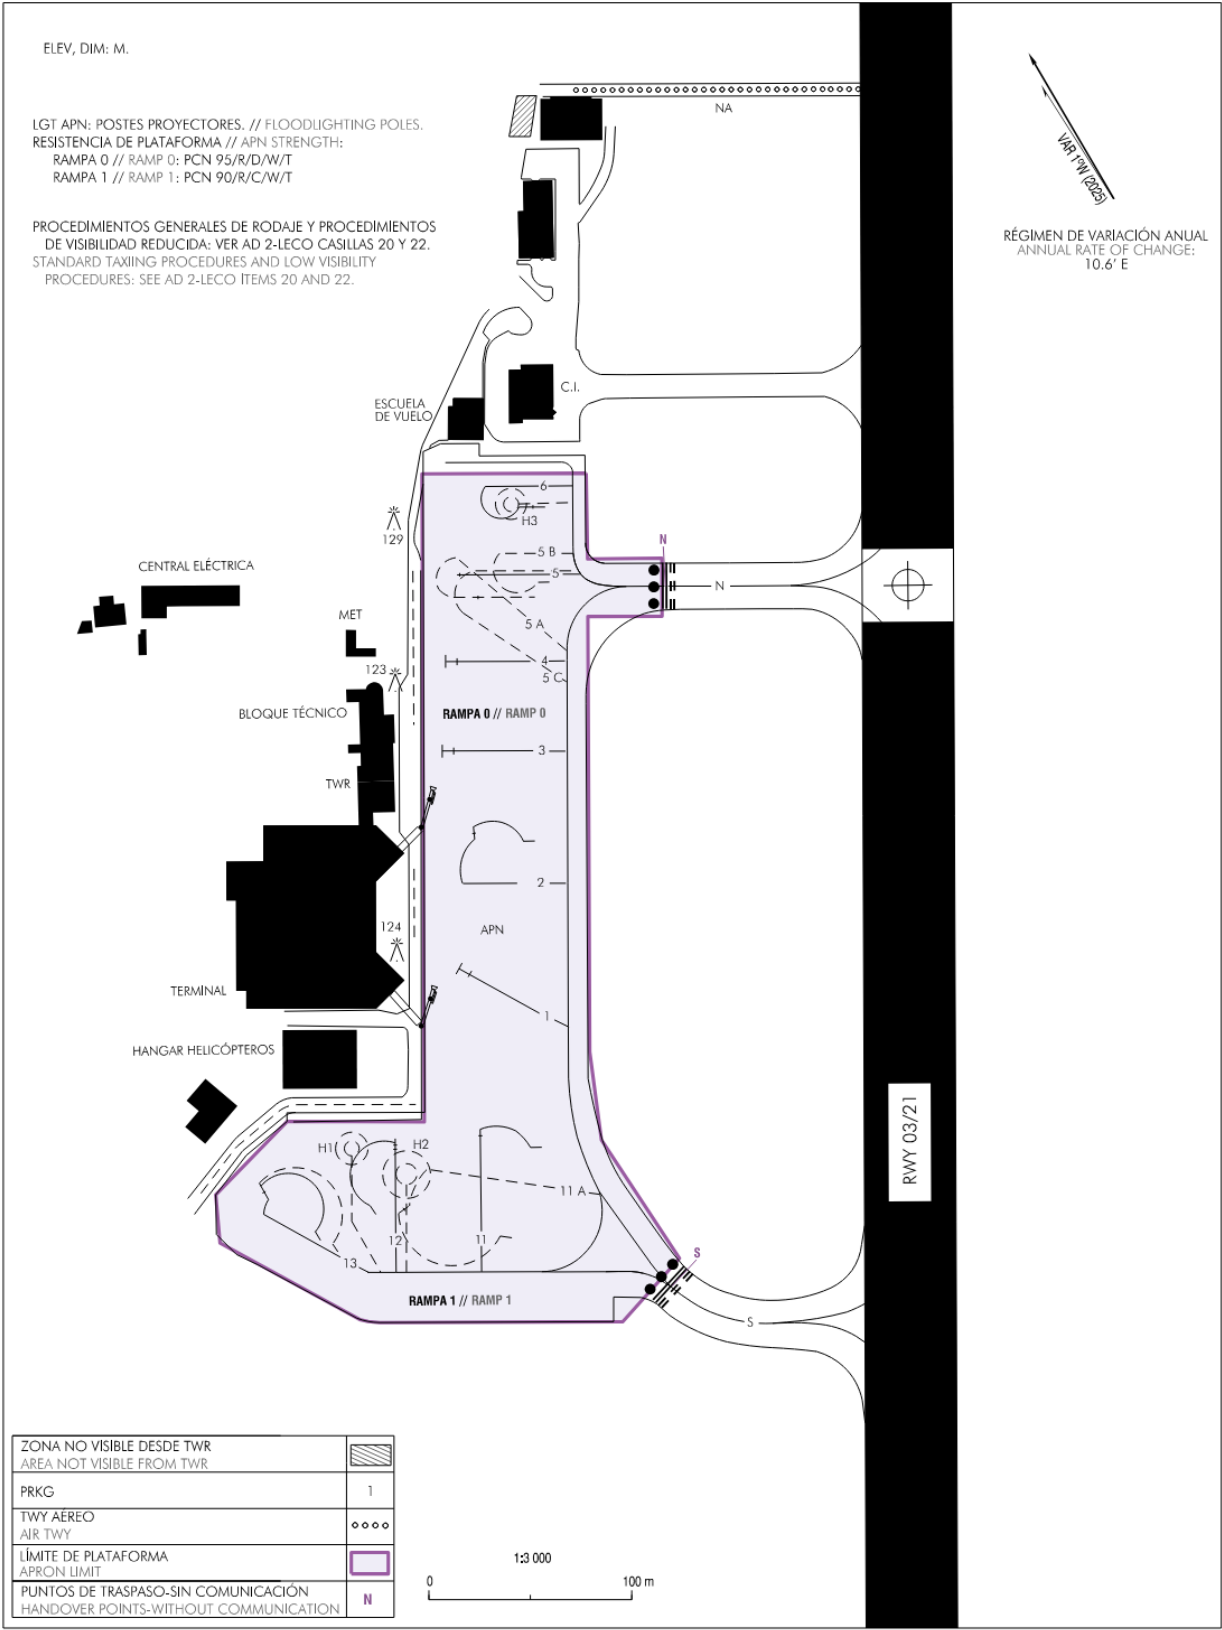

EDIFICIO ESCUELA DE VUELO  
FLIGHT TRAINING SCHOOL BUILDING

CAMBIOS:  
CHANGES

CARACTERÍSTICAS DE LOS PUESTOS DE ESTACIONAMIENTO

AIRCRAFT STANDS CHARACTERISTICS

| PRKG | RAMPA | COORD                  | SALIDA | MAX_ACFT   | APROAR  | OBSERVACIONES   |
|------|-------|------------------------|--------|------------|---------|---|
| PRKG | RAMP  | COORD                  | EXIT   | MAX_ACFT   | NOSE_TO | REMARKS   |
| 1    | 0     | 431806.11N 0082251.32W | R      | MD88       | –       | 400 Hz   |
| 2    | 0     | 431807.59N 0082249.05W | A      | B738       | –       | 400 Hz   |
| 3    | 0     | 431809.11N 0082248.98W | R      | MD88       | –       | 400 Hz   |
| 4    | 0     | 431810.24N 0082247.72W | R      | B738       | –       | –   |
| 5    | 0     | 431811.26N 0082246.38W | R      | E190       | –       | INCOMP. 5A, 5B, 5C   |
| 5A   | 0     | 431810.80N 0082246.29W | A      | F900       | –       | INCOMP. 5, 5C MAX SPAN 19 m   |
| 5B   | 0     | 431811.19N 0082245.32W | A      | F900       | –       | INCOMP. 5, 5C MAX SPAN 19 m (1)   |
| 5C   | 0     | 431810.81N 0082245.21W | A      | E190       | –       | INCOMP. 5, 5A, 5B INCOMP. entrada si PRKG 4 está ocupado // entry if PRKG 4 is occupied.                                                                                              |
| 6    | 0     | 431811.59N 0082244.24W | A      | G200       | –       | INCOMP. H3 MAX SPAN 18 m   |
| 11   | 1     | 431803.39N 0082252.36W | A      | MD88       | –       | INCOMP. 11A, H2   |
| 11A  | 1     | 431803.01N 0082254.63W | A      | B762       | –       | INCOMP. 11, 12, H1, H2   |
| 12   | 1     | 431804.02N 0082254.02W | A      | A321       | –       | INCOMP. 11A, H1, H2   |
| 13   | 1     | 431804.41N 0082257.06W | A      | A321       | –       | INCOMP. H1   |
| H1   | 1     | 431804.28N 0082254.92W | A      | (2)        | –       | INCOMP. 11A, 12, 13<br>INCOMP. con operaciones simultáneas en H2, salvo Bell 212 y EC-225 remolcado // with simultaneous operations on H2, except for Bell 212 and EC-225 when towed. |
| H2   | 1     | 431803.47N 0082254.19W | A      | (3)        | –       | INCOMP. 11, 11A, 12<br>INCOMP. con operaciones simultáneas en H1 // with simultaneous operations on H1.                                                                               |
| H3   | 0     | 431811.81N 0082244.63W | A      | EC-145 (4) | –       | INCOMP. 6<br>INCOMP. con aeronaves con calle de entrada a hangar escuela de vuelo // with aircraft using the taxiway leading to the flight school hangar.                             |

Observaciones:

- (1)

Salida regulada por procedimiento con PRKG 5A ocupado.
- (2)

Helicóptero máximo para rodaje aéreo EC-145 y para rodaje terrestre A-109.
- (3)

Helicóptero máximo para rodaje aéreo Bell 212 y para rodaje terrestre S-70.
- (4)

Helicóptero máximo para rodaje aéreo, sin especificar para rodaje terrestre.

Remarks:

- (1)

Exit regulated by procedure with PRKG 5A occupied.
- (2)

Maximum helicopter size for air taxiing EC-145 and for ground taxiing A-109.
- (3)

Maximum helicopter size for air taxiing Bell 212 and for ground taxiing S-70.
- (4)

Maximum helicopter size for air taxiing; not specified for ground taxiing.