

CARTE DES MOUVEMENTS
A LA SURFACE
DE L'AERODROME - OACI -


ARP
33°21'51"N
007°34'54" W

ELEV
AIRE DE TRAFIC
198m

TWR 118.500 MHz / 121.000 MHz
GND(SOL): 130.600 MHz /121.700 MHz
D-ATIS: 126.300 MHz

CASABLANCA Mohammed V

ALTITUDES ET DIMENSIONS EN METRES

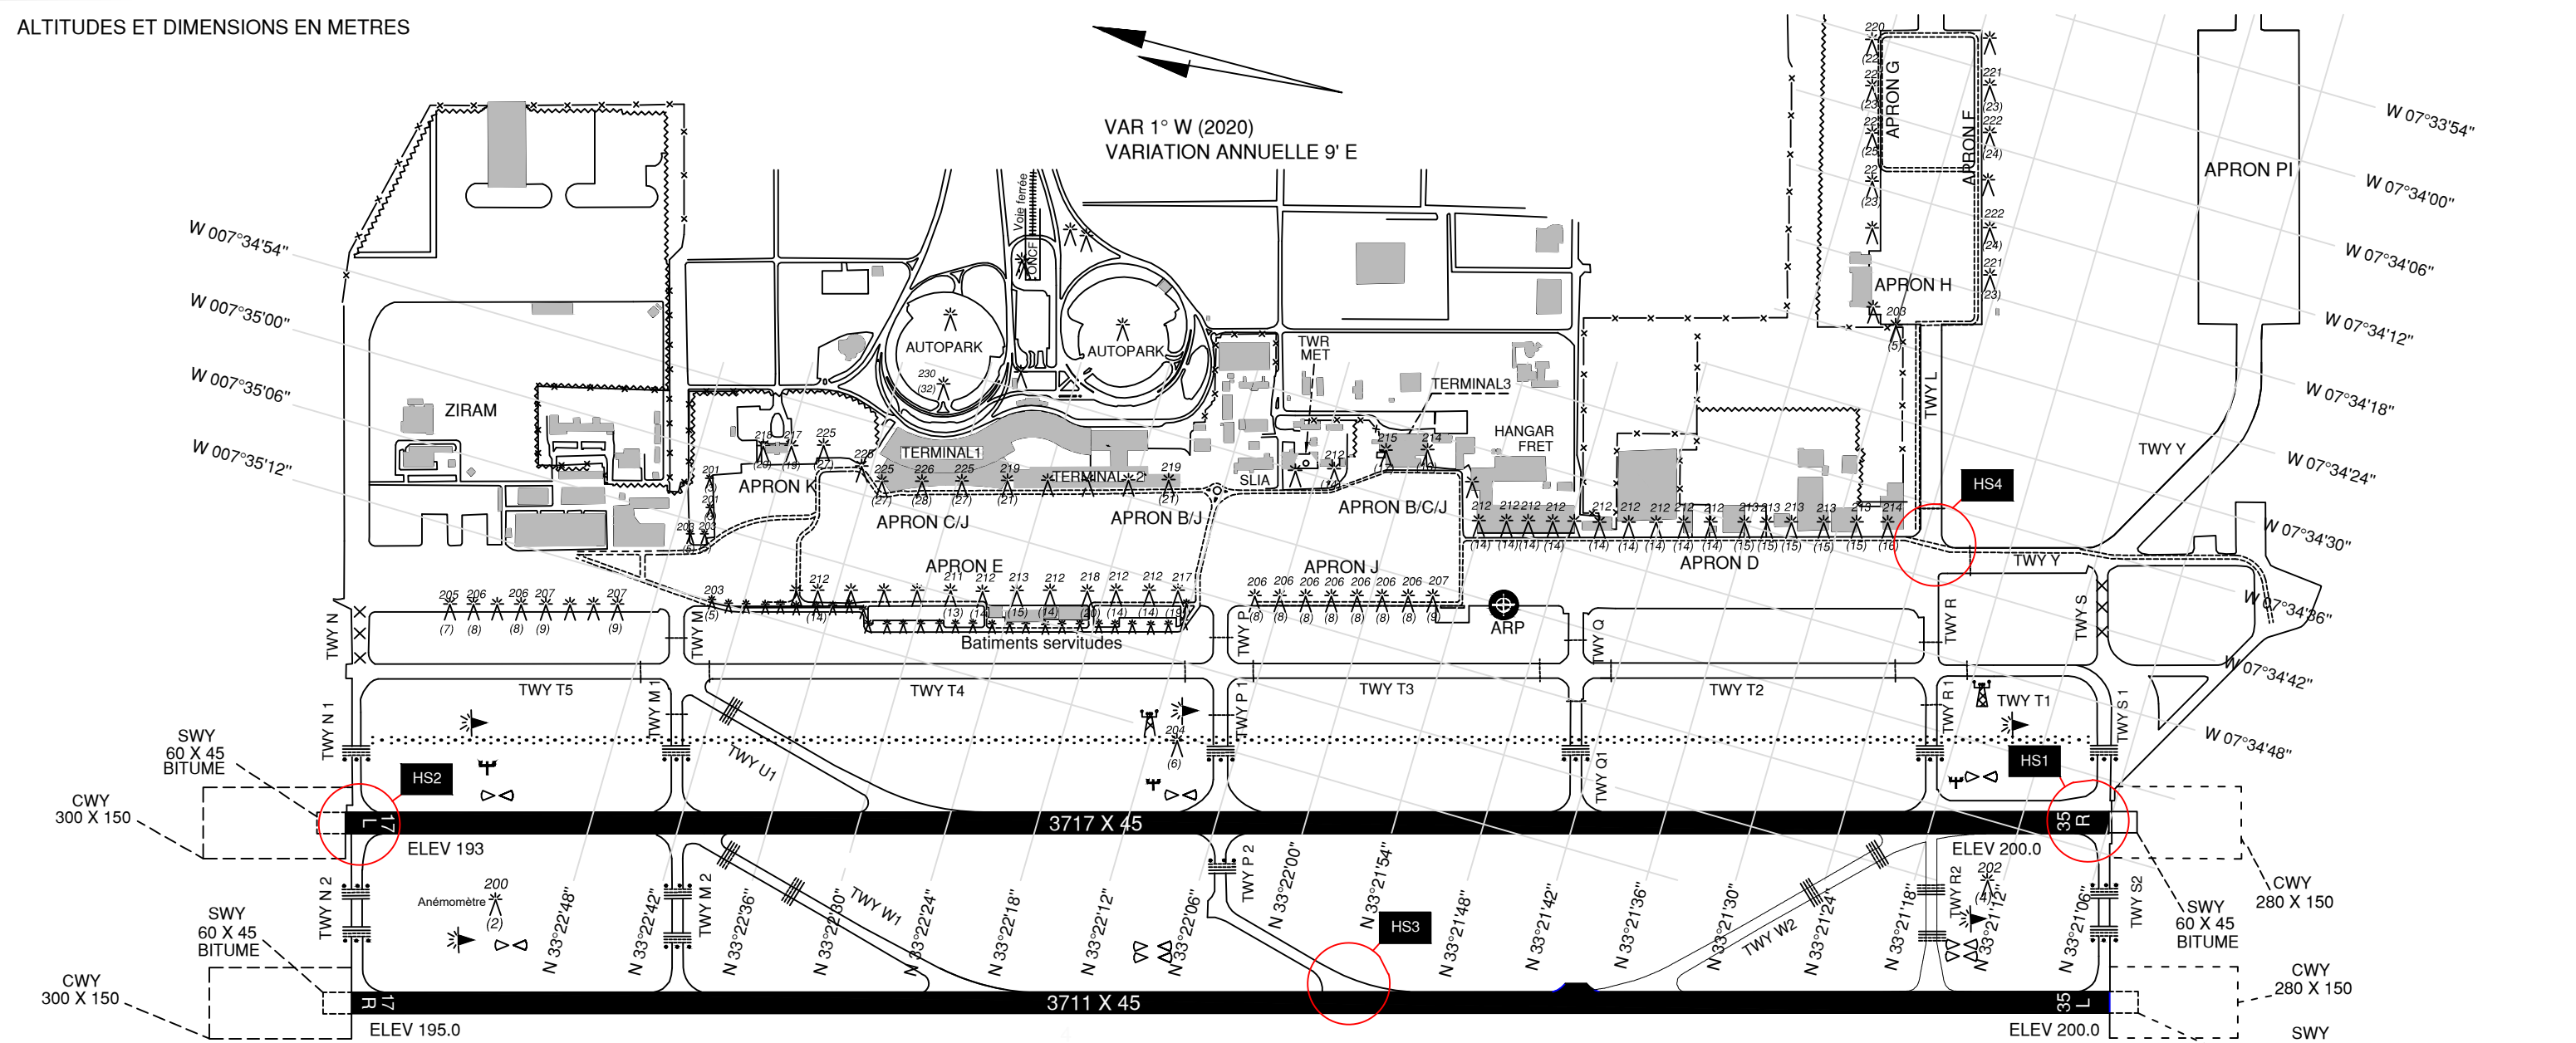

VOIES DE CIRCULATION		
TWY	LARGEURS	FORCE PORTANTE
TWY T1	23	PCN 101 R/B/W/T
TWY T2		PCN 94 F/B/W/T
TWY T3		PCN 74 F/B/W/T
TWY T4		PCN 83 F/B/W/T
TWY T5, N1		PCN 82 F/B/W/T
TWY S1		PCN 96 R/B/W/T
TWY S2		PCN 163 F/B/W/T
TWY N2		PCN 147 F/B/W/T
TWY M2		PCN 79 R/B/W/T
TWY R		PCN 79 F/B/W/T
TWY R1		PCN 53 F/B/W/T
TWY R2, W2		PCN 86 F/B/W/T

VOIES DE CIRCULATION		
TWY	LARGEURS	FORCE PORTANTE
TWY M	23	PCN 87 F/B/W/T
TWY M1, P		PCN 48 F/B/W/T
TWY P1, P2		PCN 55 F/B/W/T
TWY Q, Q1		PCN 31 F/B/W/T
TWY L		PCN 47 F/B/W/T
TWY Y		PCN 41 F/B/W/T
TWY N		PCN 18 F/B/W/T
TWY U1, W1		PCN 84 F/B/W/T
TWY S		NOT AVLB

FEUX DE VOIES DE CIRCULATION SUR TOUTES LES VOIES DE CIRCULATION SAUF TWY Y.
FEUX AXIAUX DE VOIE DE CIRCULATION SUR N1, N2, M, M1, M2, P, P1, P2, S1, S2, T1, T2, T3, T4, T5, U1, W1, W2 et R2

LEGENDE	
Manche à air (balisée)	
Diffusomètre	
Pylône d'éclairage, Antenne	
Portée visuelle de piste (RVR)	
Mur de clôture	
Clôture grillage	
Chemin de ronde	
Voies de service	
Point d'attente avant piste	
Point d'attente intermédiaire	
Feux de Barres d'arrêt	
TWY Fermé	
Parc METEO	
Batiments	
Point chauds avec ident	
Limite du service ATC(GND)	

mètres

1000000

0

500

1000

2000

3000

500

0

1000

2000

3000

pieds

HS1

Les pilotes autorisés au décollage à partir de la piste 35R/L via TWY S1et S2, prudence de ne pas confondre les points d'arrêt des pistes parallèles.

HS2

Les pilotes autorisés au décollage à partir de la piste 17L/R via TWY N1et N2 prudence de ne pas confondre entre les points d'arrêt des pistes parallèles.

HS3

Après atterrissage piste 35L, prudence TWY P2 n'est pas une sortie rapide. **Risque de confusion entre P2 et W1.**

HS4

Prudence recommandée à l'entrée du TWY R du coté des parkings D
Cause : Trafic quittant les parkings F, G & H vers TWY R .


CARTE DE STATIONNEMENT
ET D'ACCOSTAGE
D'AERONEF-OACI-

ARP
33°21'51"N
007°34'54" W

ELEV
AIRE DE TRAFIC
198m

TWR 118.500 MHz / 121.000 MHz
GND(SOL): 130.600 MHz / 121.700 MHz
D-ATIS: 126.300 MHz

CASABLANCA Mohammed V

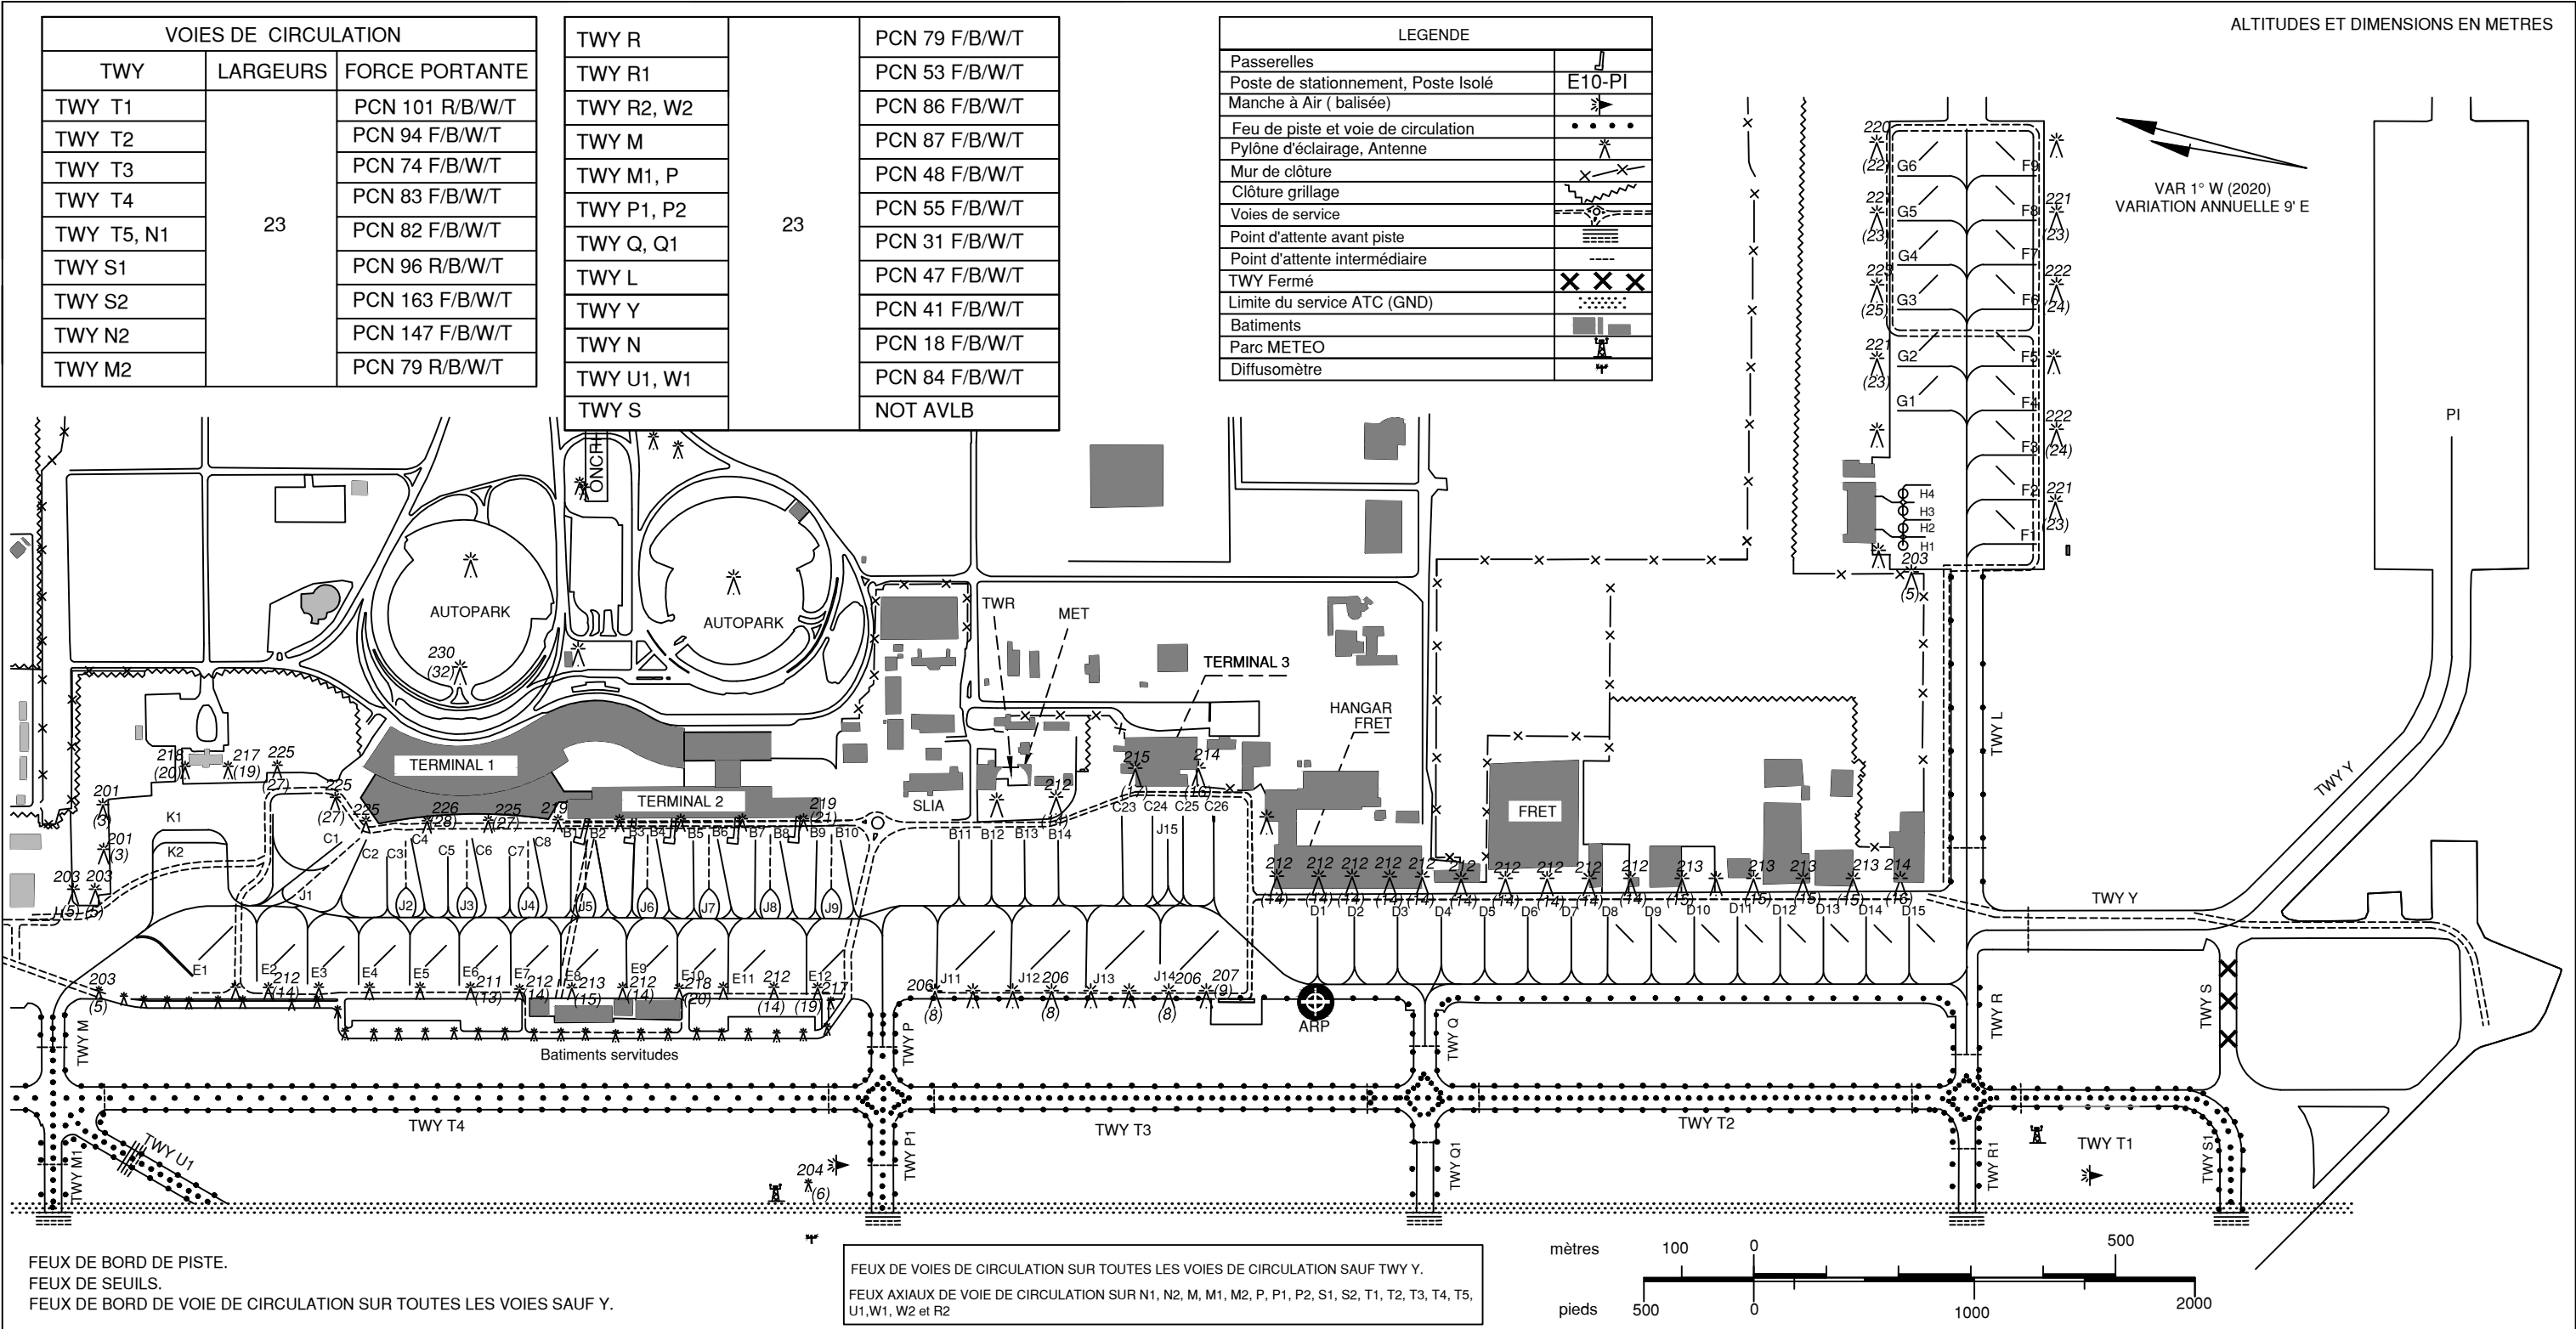

CARTE DE STATIONNEMENT
ET D'ACCOSTAGE
D'AERONEF-OACI-

ELEV
AIRE DE TRAFIC
198 m

CASABLANCA Mohammed V

COORDONNEES DES POSTES DE STATIONNEMENT D'AERONEF			ALT (m)	FORCE PORTANTE
B1	33° 22' 24.43"N	07° 34' 57.36"W	196,13	PCN 51 R/B/W/T
B2	33° 22' 23.56"N	07° 34' 56.26"W	196	PCN 53 R/B/W/T
B3	33° 22' 21.81"N	07° 34' 56.30"W	196,09	
B4	33° 22' 20.95"N	07° 34' 55.22"W	195,96	
B5	33° 22' 19.13"N	07° 34' 55.52"W	196,07	
B6	33° 22' 18.38"N	07° 34' 54.17"W	196,05	
B7	33° 22' 16.48"N	07° 34' 54.60"W	196,19	
B8	33° 22' 15.65"N	07° 34' 53.43"W	196,03	
B9	33° 22' 13.84"N	07° 34' 53.69"W	196,13	PCN 53 R/B/W/T
B10	33° 22' 12.94"N	07° 34' 52.70"W	195,76	PCN 34 F/B/W/T
B11	33° 22' 06.99"N	07° 34' 51.18"W	195,4	
B12	33° 22' 05.58"N	07° 34' 50.71"W	195,37	
B13	33° 22' 04.15"N	07° 34' 50.25"W	195,33	
B14	33° 22' 02.70"N	07° 34' 49.78"W	195,22	
C1	33° 22' 34.51"N	07° 34' 59.90"W	195,36	PCN 70 R/B/W/T
C2	33° 22' 33.46"N	07° 34' 59.49"W	195,53	PCN 67 R/B/W/T
C3	33° 22' 32.36"N	07° 35' 00.03"W	195,46	
C4	33° 22' 31.54"N	07° 34' 58.76"W	195,65	
C5	33° 22' 29.73"N	07° 34' 59.12"W	195,78	
C6	33° 22' 28.91"N	07° 34' 57.84"W	195,72	
C7	33° 22' 27.08"N	07° 34' 58.20"W	196,00	
C8	33° 22' 26.27"N	07° 34' 56.93"W	196,91	PCN 51 F/B/W/T
C23	33° 22' 01.10"N	07° 34' 47.43"W	195,91	
C24	33° 21' 59.77"N	07° 34' 46.97"W	196,41	
C25	33° 21' 58.45"N	07° 34' 46.51"W	196,71	
C26	33° 21' 57.13"N	07° 34' 46.06"W	196,93	
D1	33° 21' 51.47"N	07° 34' 49.37"W	196,22	PCN 41 F/B/W/T
D2	33° 21' 49.89"N	07° 34' 48.84"W	196,08	PCN 55 F/B/W/T
D3	33° 21' 48.02"N	07° 34' 48.16"W	196	
D4	33° 21' 46.13"N	07° 34' 47.57"W	196,09	
D5	33° 21' 44.26"N	07° 34' 46.93"W	196,29	
D6	33° 21' 42.39"N	07° 34' 46.29"W	196,37	
D7	33° 21' 40.52"N	07° 34' 45.65"W	196,63	
D8	33° 21' 38.92"N	07° 34' 45.11"W	196,79	
D9	33° 21' 37.07"N	07° 34' 44.47"W	196,84	
D10	33° 21' 35.11"N	07° 34' 44.24"W	197,38	
D11	33° 21' 33.25"N	07° 34' 43.59"W	197,35	
D12	33° 21' 31.40"N	07° 34' 42.95"W	197,73	
D13	33° 21' 29.54"N	07° 34' 42.31"W	197,77	
D14	33° 21' 27.69"N	07° 34' 41.67"W	197,94	PCN 72 R/B/W/T
D15	33° 21' 25.84"N	07° 34' 41.02"W	198,13	
E1	33° 22' 38.77"N	07° 35' 07.24"W	195,73	
E2	33° 22' 35.64"N	07° 35' 06.77"W	195,03	
E3	33° 22' 33.42"N	07° 35' 05.98"W	194,53	
E4	33° 22' 31.26"N	07° 35' 05.30"W	193,98	
E5	33° 22' 29.09"N	07° 35' 04.57"W	194,68	
E6	33° 22' 26.85"N	07° 35' 03.77"W	195,36	
E7	33° 22' 24.69"N	07° 35' 03.08"W	195,71	
E8	33° 22' 22.48"N	07° 35' 02.54"W	195,99	
E9	33° 22' 19.65"N	07° 35' 01.59"W	195,85	
E10	33° 22' 17.47"N	07° 35' 00.85"W	195,87	
E11	33° 22' 15.27"N	07° 35' 00.08"W	195,99	
E12	33° 22' 11.91"N	07° 34' 59.01"W	195,87	

COORDONNEES DES POSTES DE STATIONNEMENT D'AERONEF			ALT (m)	FORCE PORTANTE
F1	33° 21' 26.69"N	07° 34' 18.83"W	197,8	PCN 46 R/B/W/T
F2	33° 21' 27.24"N	07° 34' 16.54"W	197,78	
F3	33° 21' 27.79"N	07° 34' 14.25"W	197,67	
F4	33° 21' 28.35"N	07° 34' 11.92"W	197,69	
F5	33° 21' 28.89"N	07° 34' 09.67"W	197,66	
F6	33° 21' 29.70"N	07° 34' 06.70"W	197,6	
F7	33° 21' 30.24"N	07° 34' 04.41"W	197,59	
F8	33° 21' 30.76"N	07° 34' 02.12"W	197,56	
F9	33° 21' 31.33"N	07° 33' 59.83"W	197,60	
G1	33° 21' 31.68"N	07° 34' 13.11"W	197,63	PCN 49 R/B/W/T
G2	33° 21' 32.22"N	07° 34' 10.80"W	197,64	
G3	33° 21' 32.93"N	07° 34' 07.88"W	197,65	
G4	33° 21' 33.49"N	07° 34' 05.57"W	197,67	
G5	33° 21' 34.05"N	07° 34' 03.29"W	197,66	
G6	33° 21' 34.60"N	07° 34' 00.99"W	197,69	
J1	33° 22' 33.77"N	07° 34' 59.52"W	195,51	PCN 70 R/B/W/T
J2	33° 22' 31.79"N	07° 34' 58.76"W	195,64	PCN 67 R/B/W/T
J3	33° 22' 29.16"N	07° 34' 57.85"W	195,72	
J4	33° 22' 26.52"N	07° 34' 56.93"W	195,76	PCN 51 R/B/W/T
J5	33° 22' 24.00"N	07° 34' 56.27"W	196,02	PCN 53 R/B/W/T
J6	33° 22' 21.33"N	07° 34' 55.40"W	195,92	
J7	33° 22' 18.68"N	07° 34' 54.51"W	196,03	PCN 47 R/B/W/T
J8	33° 22' 15.91"N	07° 34' 54.09"W	196,13	PCN 53 R/B/W/T
J9	33° 22' 13.38"N	07° 34' 52.72"W	195,86	PCN 42 F/B/W/T
J11	33° 22' 06.08"N	07° 34' 56.79"W	196,21	
J12	33° 22' 02.87"N	07° 34' 55.69"W	196,22	PCN 36 F/B/W/T
J13	33° 21' 59.66"N	07° 34' 54.60"W	196,31	PCN 42 F/B/W/T
J14	33° 21' 56.42"N	07° 34' 53.50"W	196,32	PCN 51 F/B/W/T
J15	33° 21' 59.14"N	07° 34' 46.67"W	196,59	PCN 61 R/B/W/T
K1	33° 22' 40.30"N	07° 35' 02.02"W	195,02	PCN 55 R/B/W/T
K2	33° 22' 40.45"N	07° 35' 01.37"W	194,85	PCN48 F/B/W/T
PI	33° 21' 07.97"N	07° 34' 10.10"W	196,60	PCN 40 R/B/W/T
H1	33° 21' 30.80"N	07° 34' 21.66"W	197,01	
H2	33° 21' 31.01"N	07° 34' 20.80"W	197,02	
H3	33° 21' 31.22"N	07° 34' 19.91"W	197,02	
H4	33° 21' 31.44"N	07° 34' 19.01"W	197	