



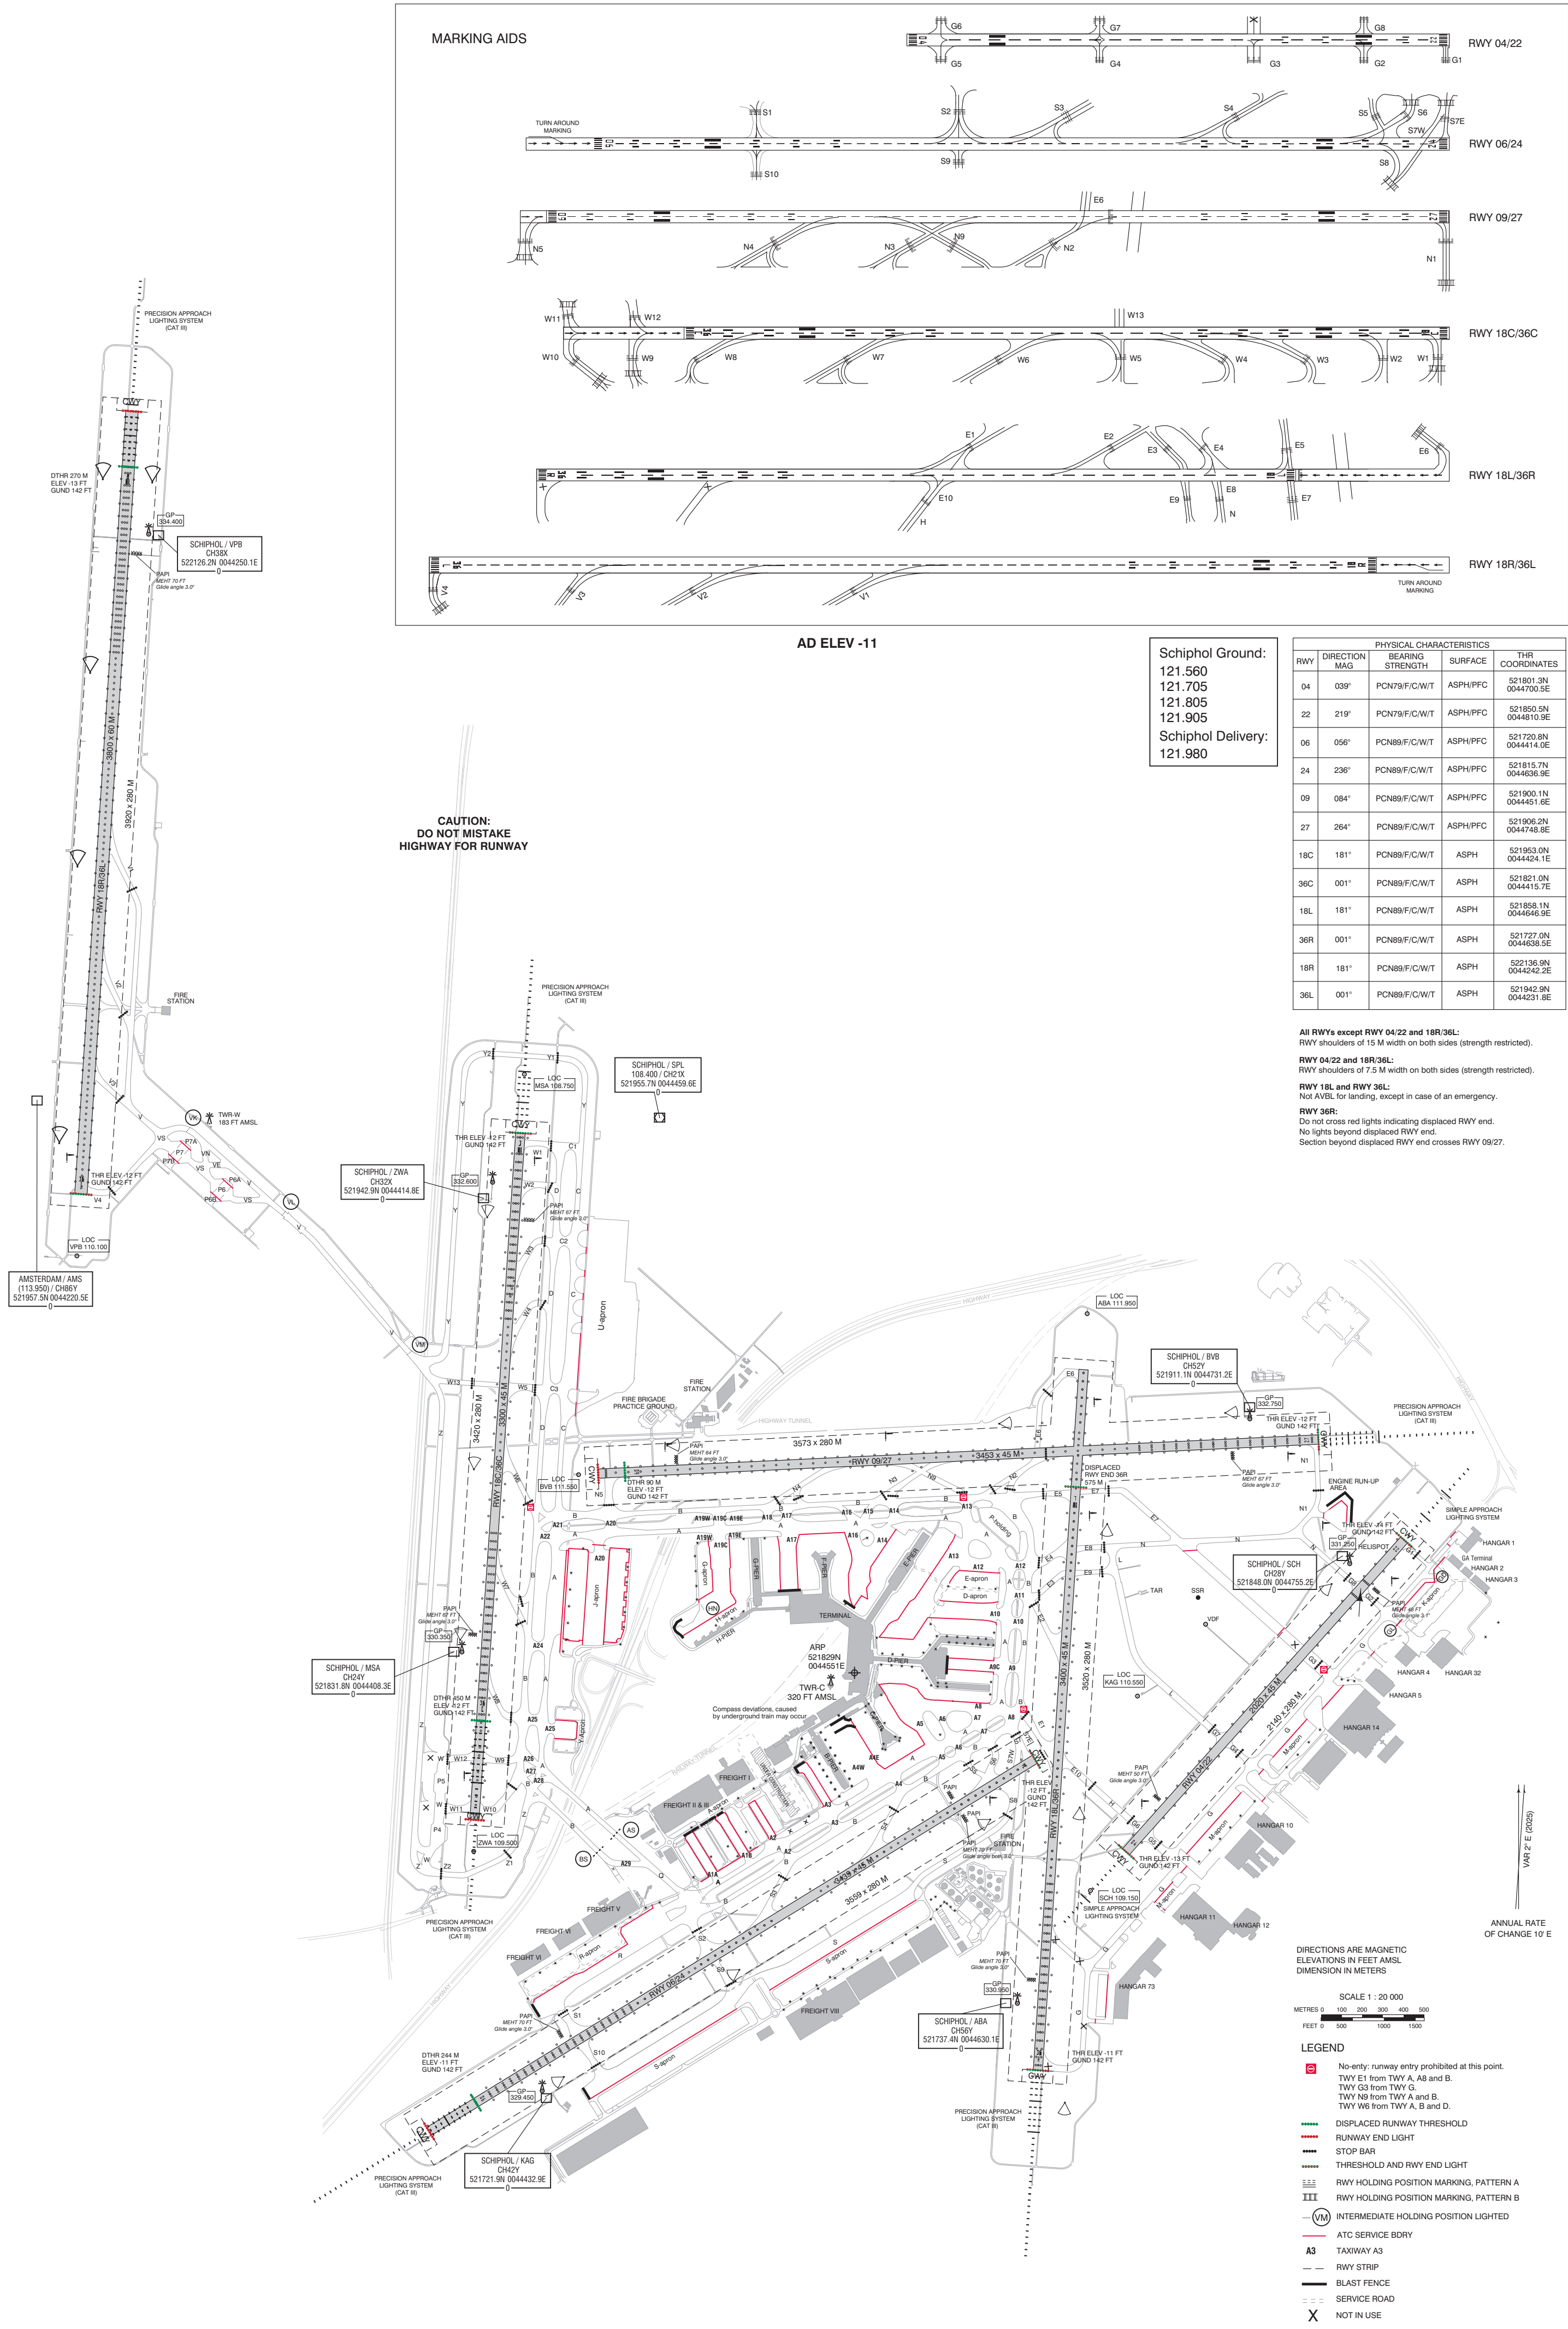

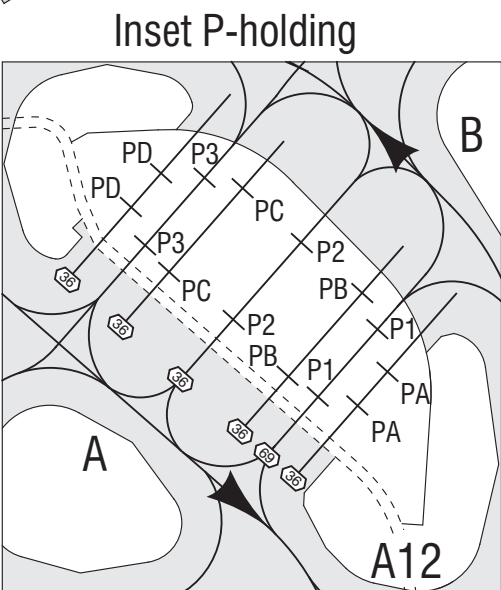

STAND	LAT	LONG	STAND	LAT	LONG	STAND	LAT	LONG	STAND	LAT	LONG
A31	521757.04N	0445411.22E	C5	521823.85N	0445596.56E	E2	521837.40N	0445596.96E	P10	521846.54N	044438.46E
A32	521758.28N	0445430.97E	C6	521823.85N	0445596.56E	E3	521839.10N	0445593.97E	P11	521846.54N	044438.28E
A33	521759.48N	044508.72E	C7	521822.26N	044558.13E	E4	521838.37N	044600.26E	P12	521843.27N	044438.16E
A34	521800.70N	044507.48E	C8	521819.54N	044554.97E	E5	521840.91N	044555.51E	P13	521840.78N	044438.28E
A41	521759.21N	044517.40E	C9	521820.42N	044600.67E	E6	521840.36N	044601.10E	P14	521839.87N	044437.85E
A42	521800.43N	044516.15E	C10	521818.54N	044556.56E	E7	521843.07N	044557.12E	P15	521838.45N	044437.72E
A43	521801.65N	044514.91E	C11	521819.74N	044604.57E	E8	521842.25N	044603.38E	P16	521835.57N	044437.45E
A44	521802.87N	044513.66E	C12	521817.08N	044557.00E	E9	521845.21N	044558.82E	R71	521739.70N	044429.11E
A45	521803.99N	044512.52E	C13	521818.46N	044604.50E	E17	521847.18N	044600.92E	R72	521740.40N	044429.56E
A46	521759.93N	044519.50E	C14	521815.82N	044558.18E	E18	521844.32N	044600.05E	R73	521740.28N	044430.61E
A51	521801.18N	044517.31N	C15	521817.31N	044604.57E	E19	521849.28N	044603.43E	R74	521741.87N	044433.36E
A53	521802.37N	044517.01E	C16	521815.76N	044600.19E	E20	521846.73N	044608.10E	R77	521743.32N	044437.10E
A54	521803.60N	044515.76E	C18	521816.84N	044601.41E	E22	521848.76N	044610.28E	R80	521745.19N	044442.02E
A55	521804.72N	044514.62E			E24	521851.01N	044612.50E	R81	521746.41N	044445.37E	
A61	521802.21N	044524.86E			E72	521843.14N	044617.82E	R82	521747.65N	044448.62E	
A62	521803.48N	044524.11E	D2	521829.44N	044558.49E	E77	521842.88N	044625.47E	S61	521721.02N	044448.45E
A63	521804.70N	044522.87E	D3	521823.60N	044558.63E	F3	521843.33N	044540.19E	S62	521722.55N	044458.29E
A64	521805.92N	044521.62E	D4	521829.48N	044602.22E	F4	521844.26N	044545.73E	S63	521721.00N	044447.15E
A65	521806.28N	044520.94E	D5	521832.62N	044601.57E	F5	521845.64N	044543.72E	S64	521725.50N	044501.08E
A71	521802.78N	044526.96E	D7	521832.34N	044604.48E	F6	521846.70N	044546.49E	S65	521727.02N	044505.02E
A72	521803.80N	044525.94E	D10	521826.62N	044607.68E	F7	521848.43N	044549.38E	S66	521729.10N	044510.45E
A73	521804.82N	044524.90E	D12	521826.96N	044609.28E	F8	521848.43N	044538.98E	S67	521730.61N	044514.39E
A74	521805.84N	044523.85E	D16	521826.12N	044612.95E	F9	521848.81N	044542.36E	S68	521732.13N	044514.39E
A75	521806.64N	044522.81E	D18	521825.05N	044615.15E	F9	521848.72N	044542.36E	S69	521733.60N	044522.16E
A81	521805.14N	044532.12E	D22	521825.96N	044617.63E	G2	521842.61N	044528.47E	S72	521737.85N	044533.34E
A82	521807.19N	044531.05E	D23	521828.16N	044615.60E	G3	521842.61N	044528.47E	S74	521739.51N	044537.30E
A83	521807.19N	044530.05E	D24	521825.89N	044619.80E	G4	521841.64N	044522.63E	S77	521740.51N	044540

No-entry: runway entry prohibited at this point.

TWY E1 from TWY A, A8 and B.

TWY N9 from TWY A and B.

TWY W6 from TWY A, B and D.

MAX WINGSPAN 35 M, LIMITED ENTRY

CROSSING VEHICLES

STOP BAR

BLAST FENCE

ATC SERVICE BDRY

STANDARD TAXI ROUTING,
UNLESS OTHERWISE INSTRUCTED BY ATC.

ALL OTHER ROUTES MAY BE USED

TWO-WAY AT ATC DISCRETION ONLY.

INTERMEDIATE HOLDING POSITION