
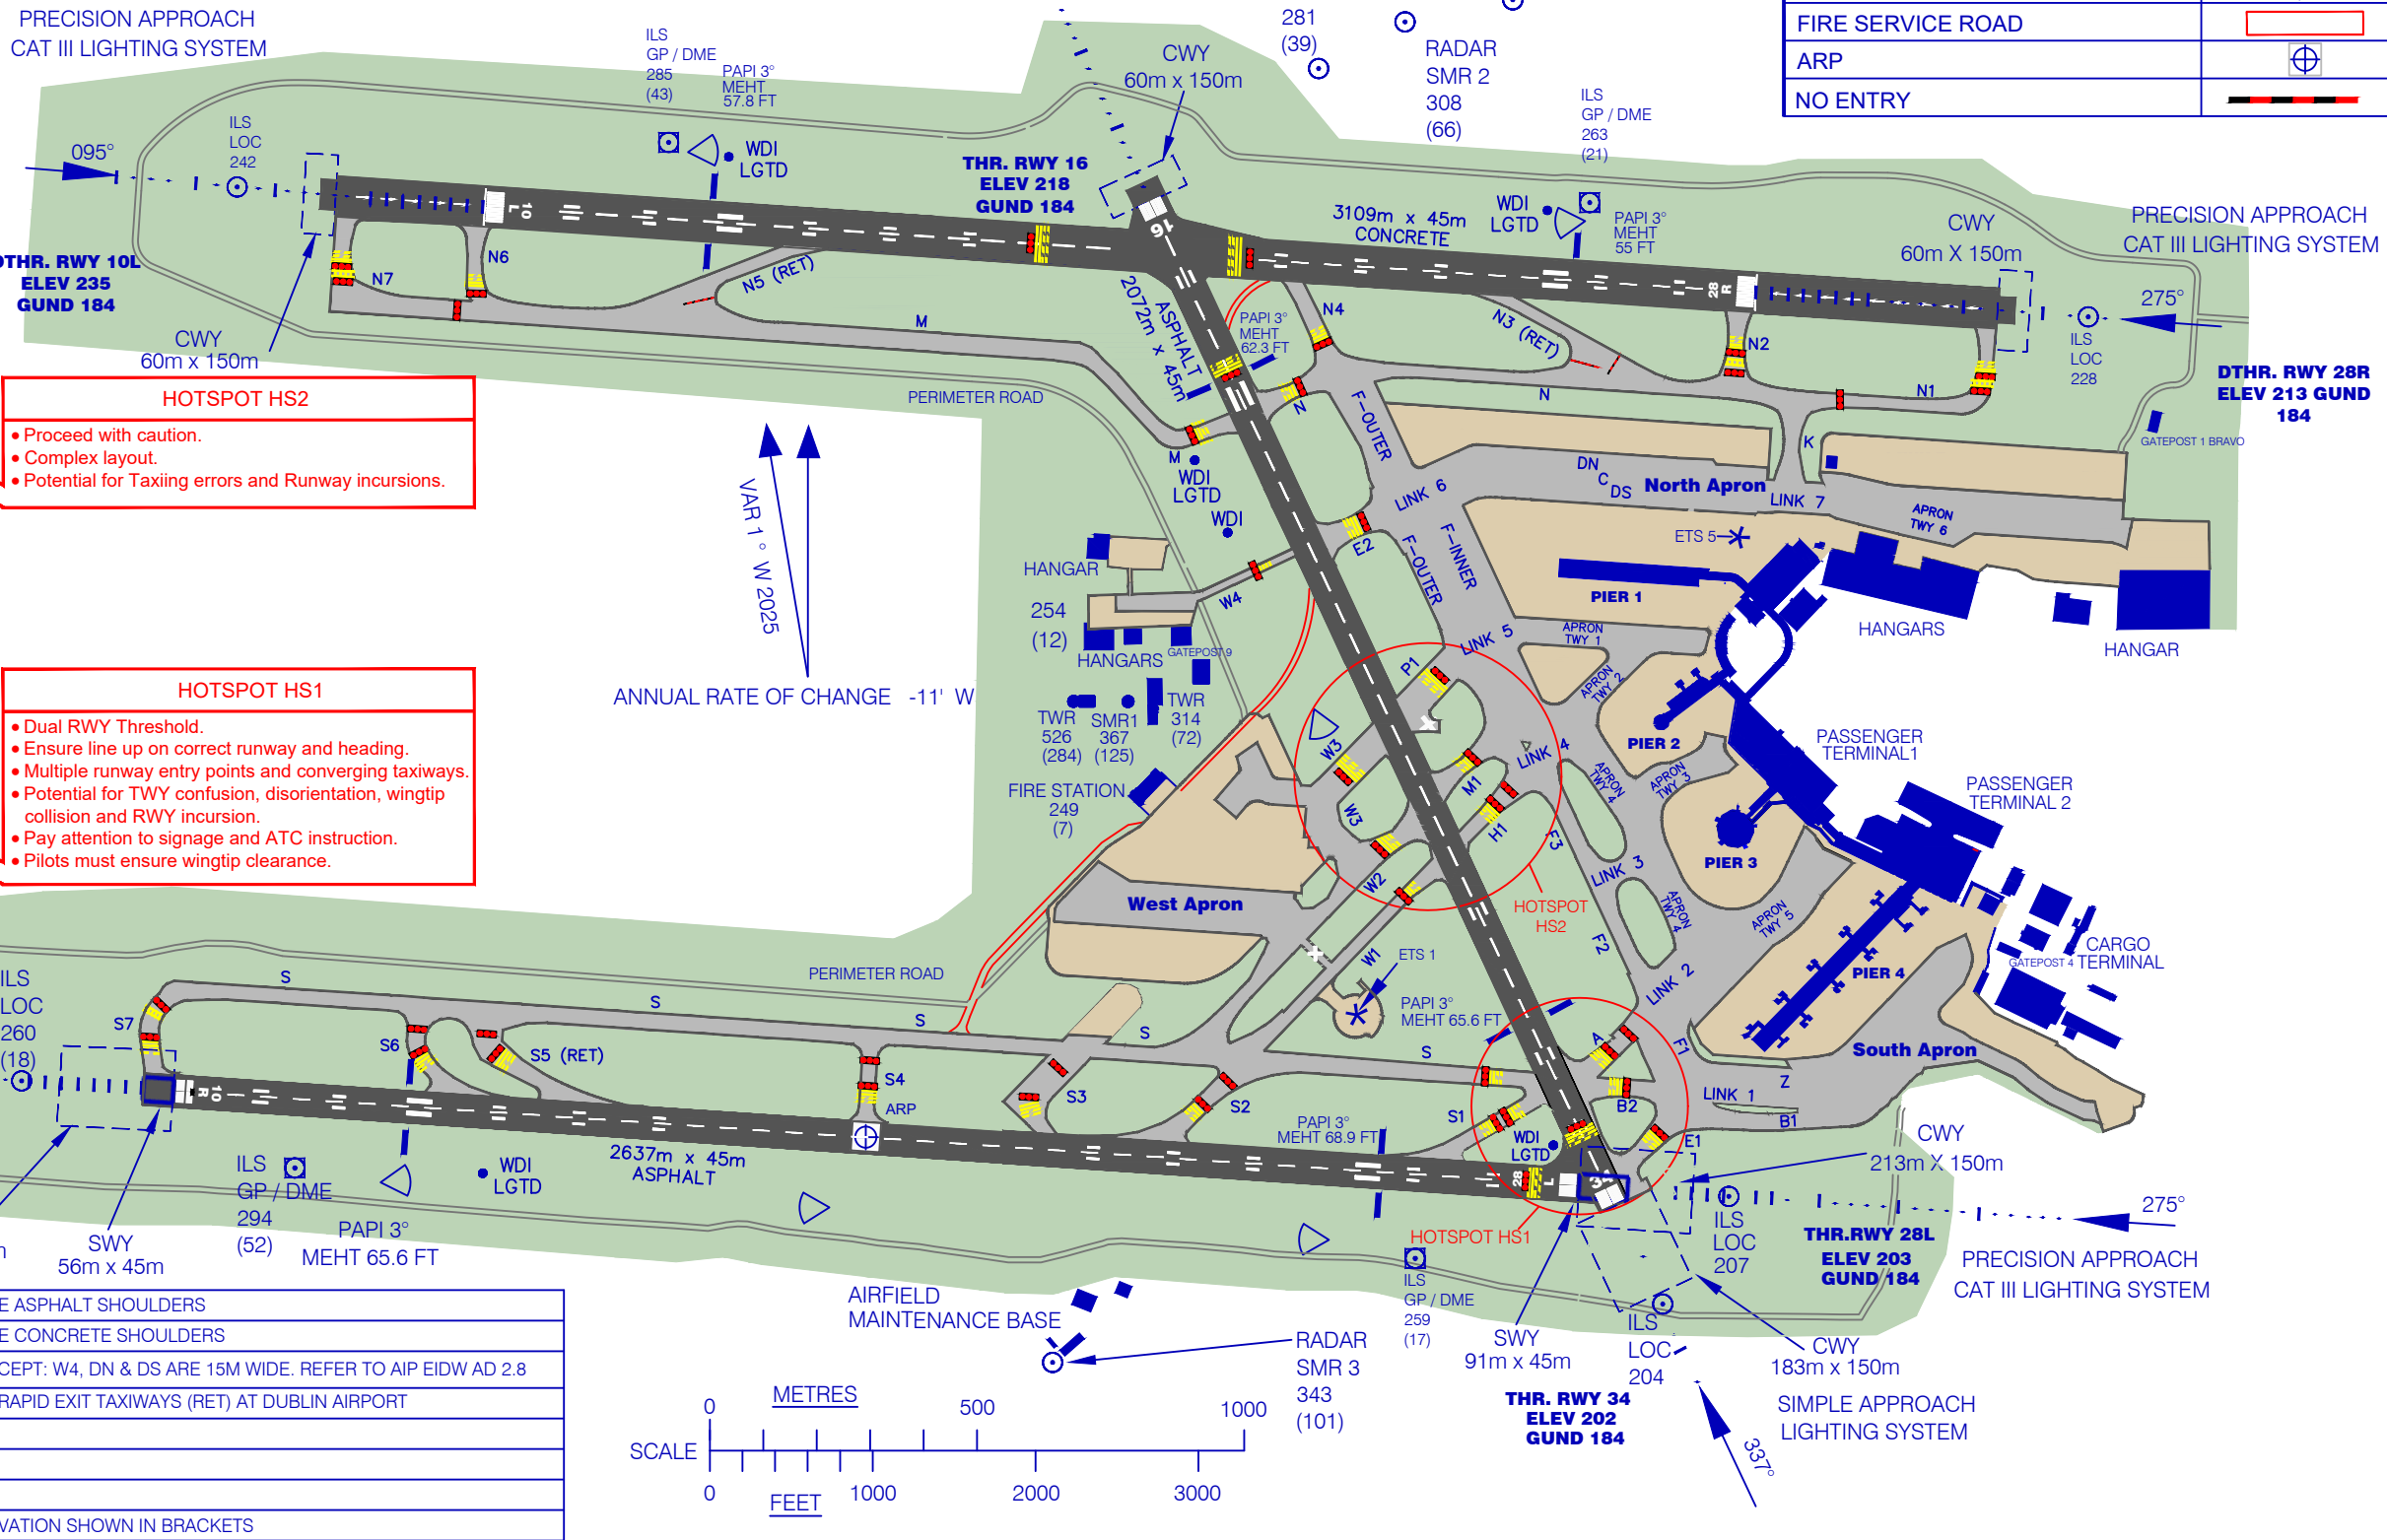


AERODROME CHART - ICAO		53 25 17 N		TWR 118.600MHz ATIS 124.530	
		006 16 12 W		GND 121.800MHz CLEARANCE DELIVERY 122.985	
		ELEV 243 FT		GND 125.885MHz	
RWY	DIRECTION	THR		BEARING STRENGTH	
10R	95°	53 25 20.75 N	006 17 24.27 W	PCR 910/R/B/W/T ASPH	
28L	275°	53 25 12.94 N	006 15 02.08 W		
16	157°	53 26 13.16 N	006 15 43.12 W	PCR 3020/F/B/W/T ASPH	
34	337°	53 25 11.66 N	006 14 58.54 W		
10L	95°	53 26 13.79 N	006 16 50.22 W	PCR 1140/R/C/W/T CONC	
28R	275°	53 26 06.73 N	006 14 41.87 W		

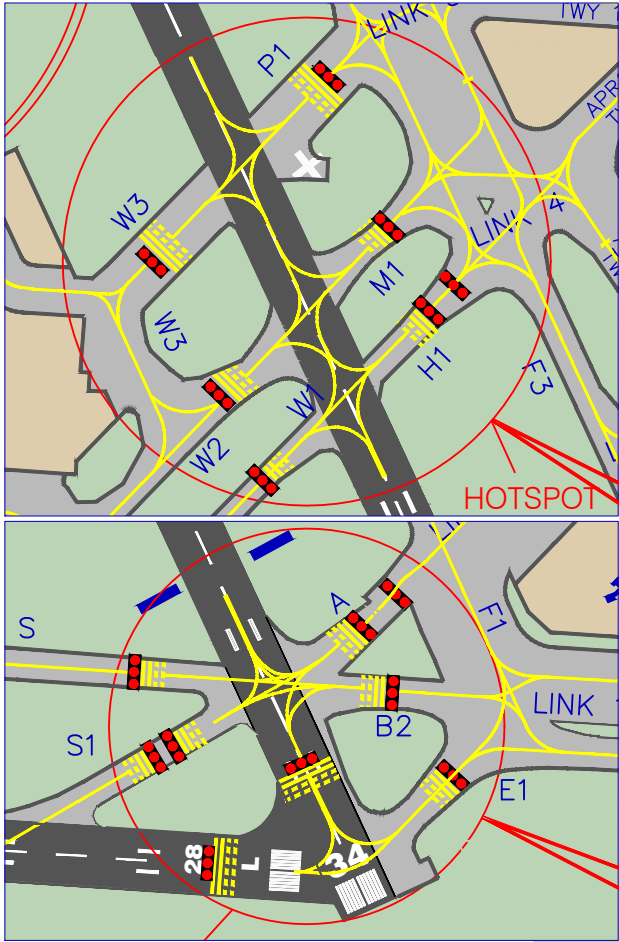


AIP IRELAND
AIRCRAFT PARKING / DOCKING CHART - ICAO

APRON ELEV.
220 FT

TWR 118.600MHz ATIS 124.530
GND 121.800MHz CLEARANCE DELIVERY 122.985
GND 125.885MHz

EIDW AD 2.24-2
DUBLIN AIRPORT/ IRELAND

CHANGES: Removal of TWY T and reintroduction of TWY B1 and TWY Z. introduction of self-manoeuvring stands 131S, 132S, 133S, 134S, 135S and 136S. Crossing point removed and ATC service boundary relocated to between stands 125-126. Coordinates updated for stands 200T, 615C, 619C, 620C and 621C. Removal of stands 618L, 618C and 618R. Removal of West Apron road crossing. Hangars on the West Apron labelled A-D, hangars on North Apron labelled 1-6. PCRs updated on TWYs B1, E2, F1, N4, S2, S3, Z, Link 7, AT6 and North Apron. Addition of CAT I/II/III co-located runway holding position at TWY E1. Removal of lead in lines to Hangar 6. SLC Geomatic Solutions.

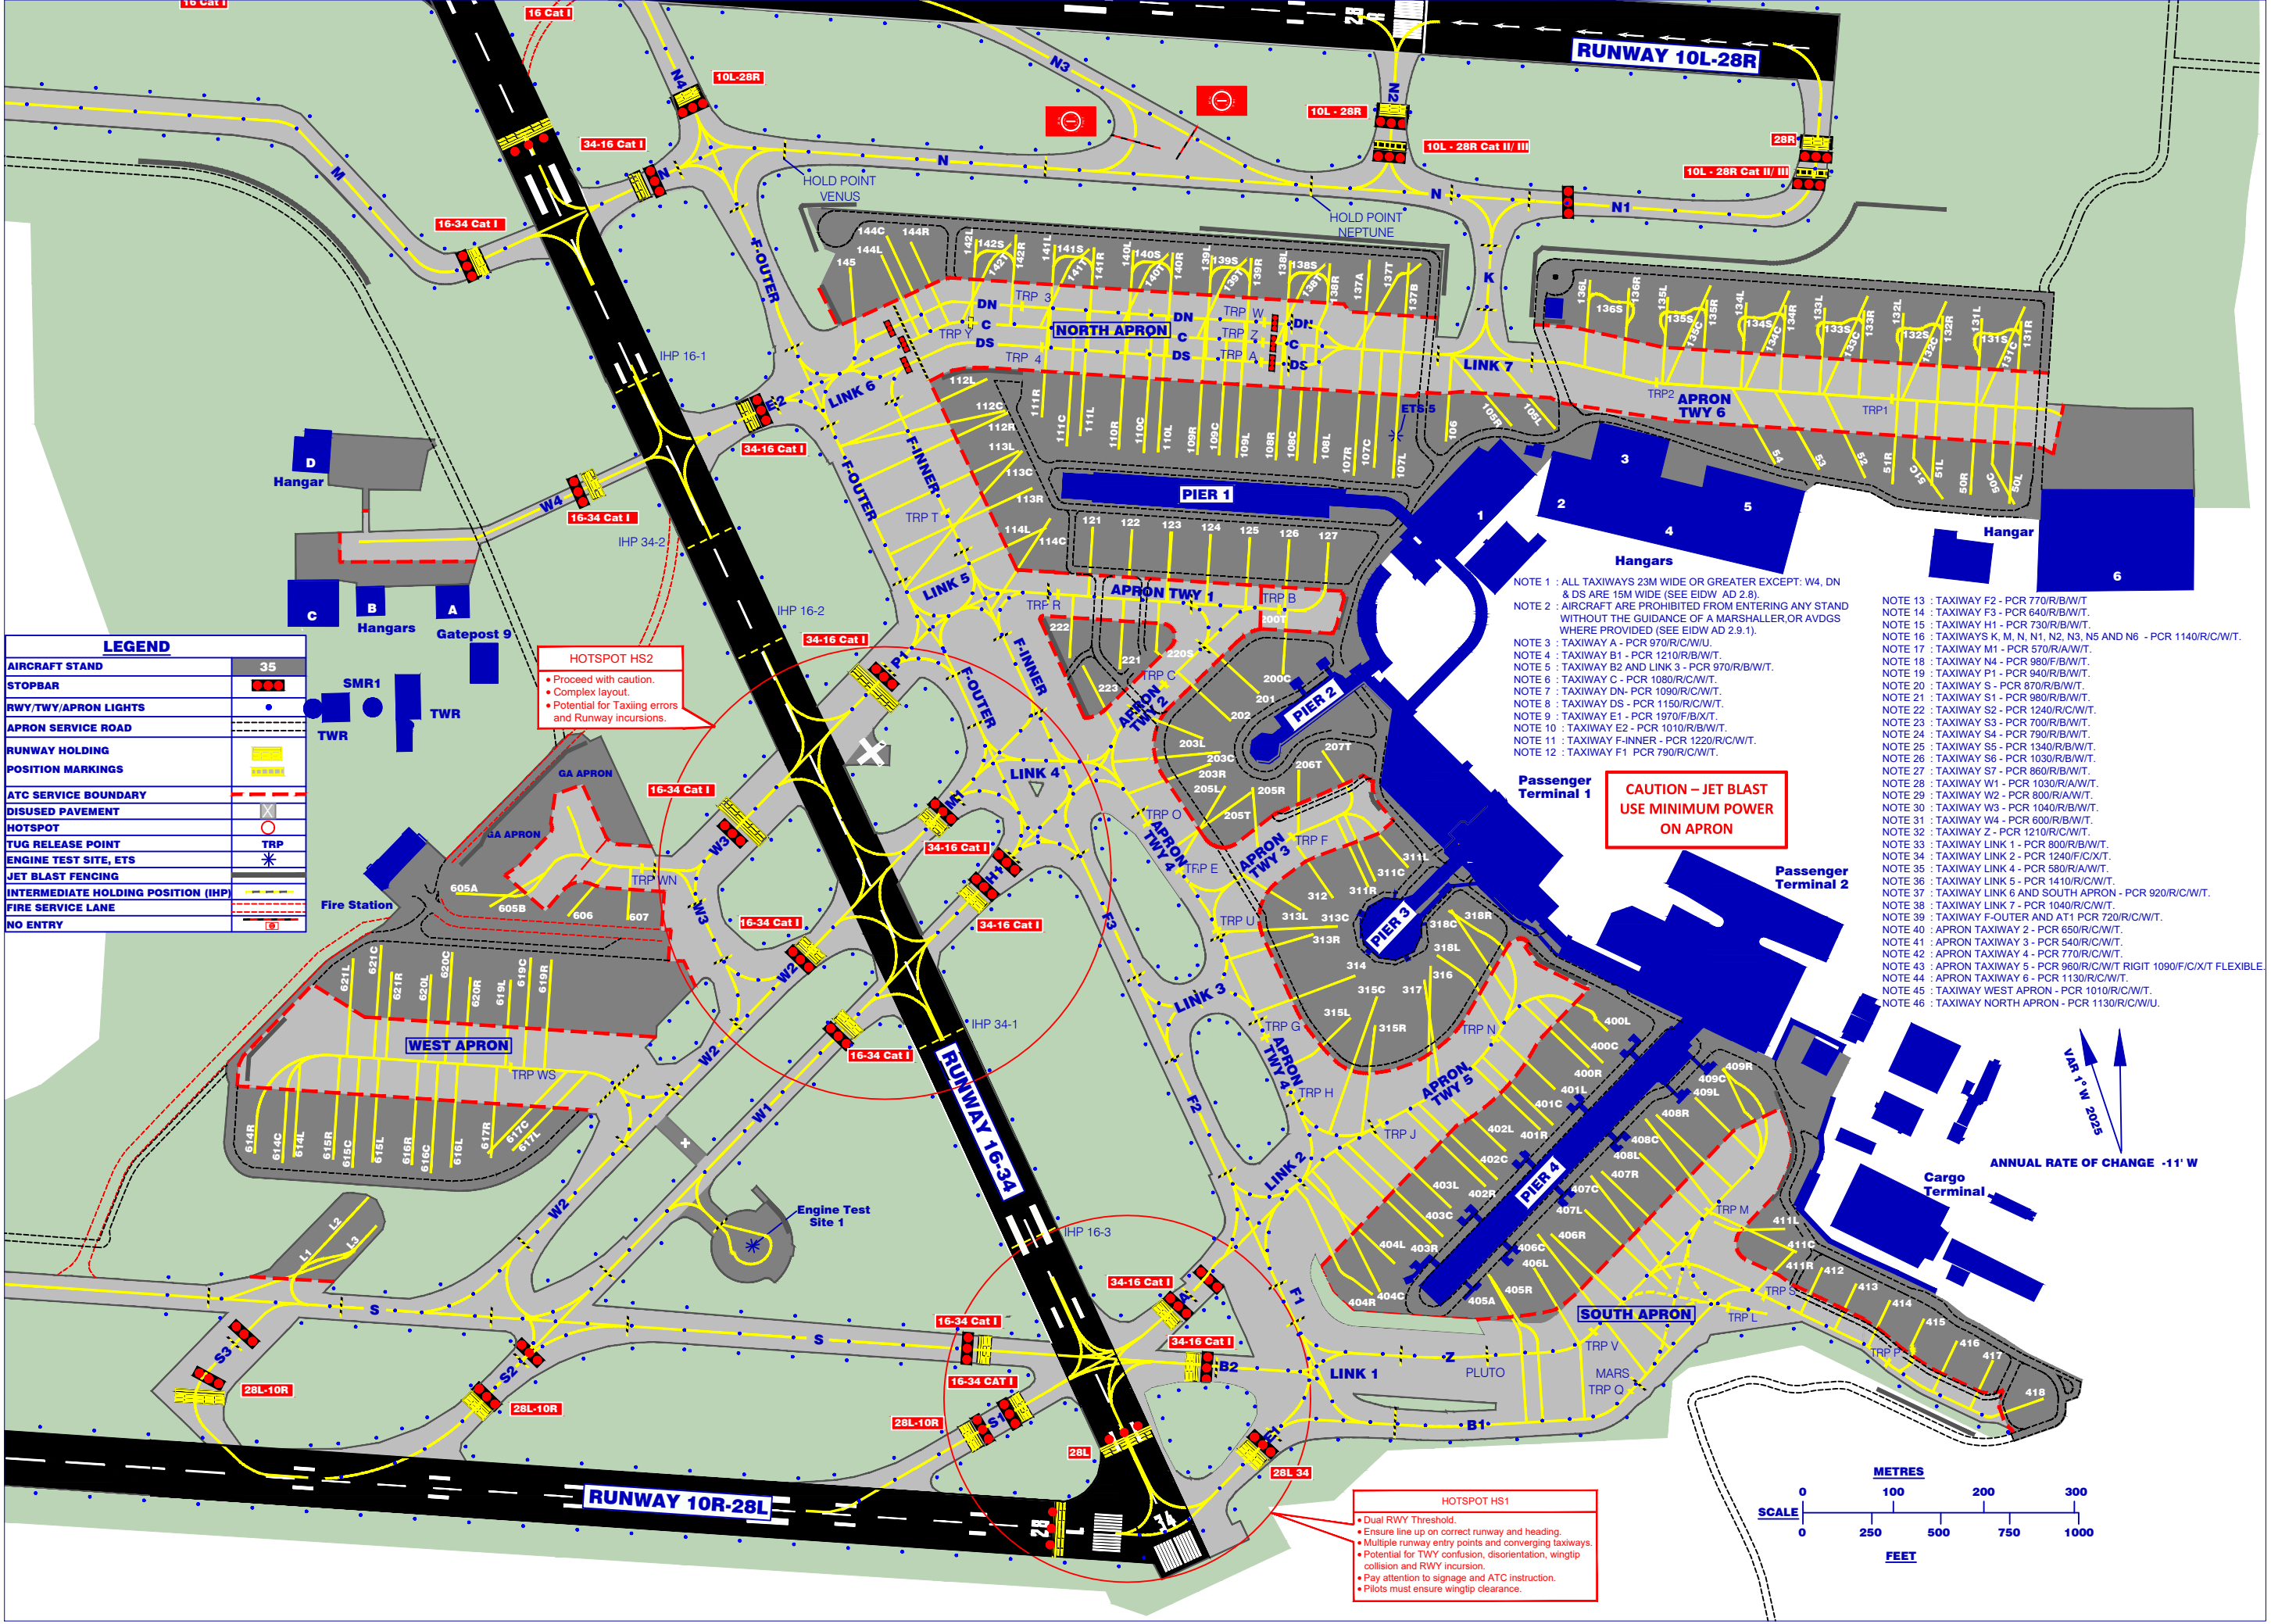

INS CHECK POINTS

Stand	Latitude	Longitude	Max Wingspan	Max Length	Conditions	Remarks	Stand	Latitude	Longitude	Max Wingspan	Max Length	Conditions	Remarks
50L	53 25 49.68 N	006 14 07.63 W	36.00m	44.51m	TAXI IN, PUSH OUT.	STAND 50C VACANT.	205L	53 25 39.55 N	006 14 55.09 W	36.00m	44.51m	TAXI IN, PUSH OUT.	STANDS 205T VACANT.
50C	53 25 49.21 N	006 14 07.66 W	65.00m	63.73m	TAXI IN, PUSH OUT.	STANDS 50L, 50R VACANT	205R	53 25 39.49 N	006 14 53.41 W	35.92m	39.50m	TAXI IN, PUSH OUT.	STAND 205T VACANT.
50R	53 25 49.81 N	006 14 09.98 W	36.00m	44.51m	TAXI IN, PUSH OUT.	STAND 50C VACANT	206T	53 25 40.08 N	006 14 50.63 W	34.10m	37.60m	TAXI IN, PUSH OUT.	
51L	53 25 49.94 N	006 14 12.32 W	36.00m	44.51m	TAXI IN, PUSH OUT.	STAND 51C VACANT.	207T	53 25 40.75 N	006 14 49.19 W	35.92m	44.51m	TAXI IN, PUSH OUT.	
51C	53 25 49.44 N	006 14 11.98 W	65.00m	66.61m	TAXI IN, PUSH OUT.	STANDS 51L, 51R VACANT	220S	53 25 44.48 N	006 14 59.00 W	27.05m	27.20m	SELF MANOEUVRING.	
51R	53 25 50.07 N	006 14 14.67 W	36.00m	44.51m	TAXI IN, PUSH OUT.	STAND 51C VACANT	221	53 25 44.14 N	006 15 01.17 W	35.80m	44.51m	TAXI IN, PUSH OUT.	
52	53 25 50.29 N	006 14 16.53 W	36.00m	44.51m	TAXI IN, PUSH OUT.		222	53 25 44.55 N	006 15 04.01 W	35.92m	39.48m	TAXI IN, PUSH OUT.	
53	53 25 50.61 N	006 14 19.30 W	36.00m	37.57m	TAXI IN, PUSH OUT.		223	53 25 43.74 N	006 15 03.19 W	35.80m	44.51m	TAXI IN, PUSH OUT.	
54*	53 25 50.91 N	006 14 21.96 W	27.10m	27.20m	TAXI IN, PUSH OUT.	STAND VACANT TO ALLOW AIRCRAFT ENTRY/EXIT TO HANGAR	311L	53 25 36.52 N	006 14 44.26 W	34.10m	37.60m	TAXI IN, PUSH OUT.	STANDS 311C VACANT.
105L	53 25 52.26 N	006 14 35.12 W	27.05m	28.58m	TAXI IN, PUSH OUT.		311C	53 25 36.05 N	006 14 46.58 W	41.10m	47.40m	TAXI IN, PUSH OUT.	STAND 311L, 311R VACANT.
105R	53 25 52.41 N	006 14 37.71 W	27.05m	28.58m	TAXI IN, PUSH OUT.		311R	53 25 35.85 N	006 14 46.66 W	36.00m	45.10m	TAXI IN, PUSH OUT.	STANDS 311C VACANT.
106	53 25 51.98 N	006 14 41.32 W	36.00m	44.51m	TAXI IN, PUSH OUT.		312	53 25 35.49 N	006 14 48.80 W	41.10m	47.40m	TAXI IN, PUSH OUT.	
107L	53 25 50.70 N	006 14 44.54 W	36.00m	44.51m	TAXI IN, PUSH OUT.	STAND 107C VACANT.	313L	53 25 35.07 N	006 14 50.73 W	36.00m	39.50m	TAXI IN, PUSH OUT.	STANDS 313C VACANT.
107C	53 25 51.10 N	006 14 45.86 W	65.00m	73.86m	TAXI IN, PUSH OUT.	STANDS 107L, 107R VACANT.	313C	53 25 34.46 N	006 14 48.44 W	65.00m	74.00m	TAXI IN, PUSH OUT.	STAND 313L, 313R VACANT.
107R	53 25 50.84 N	006 14 46.88 W	36.00m	44.51m	TAXI IN, PUSH OUT.	STAND 107C VACANT.	313R	53 25 34.20 N	006 14 50.02 W	35.80m	44.51m	TAXI IN, PUSH OUT.	STANDS 313C VACANT.
108L	53 25 51.05 N	006 14 49.22 W	36.00m	47.00m	TAXI IN, PUSH OUT.	STAND 108C VACANT.	314	53 25 32.68 N	006 14 47.57 W	64.80m	66.90m	TAXI IN, PUSH OUT.	MAX WINGSPAN 47.60M WHEN STAND 315L OCCUPIED.
108C	53 25 51.15 N	006 14 50.30 W	65.00m	75.40m	TAXI IN, PUSH OUT.	STANDS 108R, 108L VACANT.	315L	53 25 31.17 N	006 14 47.91 W	35.80m	37.60m	TAXI IN, PUSH OUT.	STAND 315C VACANT. MAX SPAN 47.60M ON STAND 314.
108R	53 25 51.18 N	006 14 51.56 W	36.00m	47.00m	TAXI IN, PUSH OUT.	STAND 108C VACANT.	315C	53 25 31.92 N	006 14 46.29 W	65.00m	74.00m	TAXI IN, PUSH OUT.	STAND 315L, 315R VACANT.
109L	53 25 51.31 N	006 14 53.91 W	36.00m	47.00m	TAXI IN, PUSH OUT.	STAND 109C VACANT.	315R	53 25 30.89 N	006 14 46.44 W	35.80m	44.51m	TAXI IN, PUSH OUT.	STANDS 315C VACANT.
109C	53 25 51.41 N	006 14 54.96 W	65.00m	75.40m	TAXI IN, PUSH OUT.	STANDS 109R, 109L VACANT.	316	53 25 32.96 N	006 14 53.03 W	65.00m	74.00m	TAXI IN, PUSH OUT.	STAND 317, 318L VACANT.
109R	53 25 51.44 N	006 14 56.26 W	36.00m	47.00m	TAXI IN, PUSH OUT.	STAND 109C VACANT.	317	53 25 32.47 N	006 14 43.44 W	60.30m	63.70m	TAXI IN, PUSH OUT.	STANDS 316 VACANT.
110L	53 25 51.57 N	006 14 58.60 W	36.00m	47.00m	TAXI IN, PUSH OUT.	STAND 110C VACANT.	318L	53 25 33.35 N	006 14 42.63 W	41.10m	47.40m	TAXI IN, PUSH OUT.	STANDS 316, 318C VACANT.
110C	53 25 51.55 N	006 14 59.46 W	65.00m	75.40m	TAXI IN, PUSH OUT.	STANDS 110R, 110L VACANT.	318C	53 25 34.94 N	006 14 41.71 W	64.80m	66.90m	TAXI IN, PUSH OUT.	STANDS 318L, 318R VACANT. STAND 400T VACANT AT ENTRY/EXIT.
110R	53 25 51.70 N	006 15 00.95 W	36.00m	47.00m	TAXI IN, PUSH OUT.	STAND 110C VACANT.	318R	53 25 34.78 N	006 14 41.55 W	36.00m	46.70m	TAXI IN, PUSH OUT.	STAND 318C VACANT. STAND 400T VACANT AT ENTRY/EXIT.
111L	53 25 52.22 N	006 15 03.24 W	36.00m	47.00m	TAXI IN, PUSH OUT.	STAND 111C VACANT.	400L	53 25 30.50 N	006 14 32.56 W	36.00m	45.10m	TAXI IN, PUSH OUT.	STAND 400C VACANT. STAND 400T VACANT AT ENTRY/EXIT.
111C	53 25 51.86 N	006 15 04.06 W	65.00m	75.40m	TAXI IN, PUSH OUT.	STANDS 111T, 111L VACANT.	400C	53 25 29.36 N	006 14 32.88 W	65.00m	74.00m	TAXI IN, PUSH OUT.	STAND 400L, 400R VACANT. STAND 400T VACANT AT ENTRY/EXIT.
111R	53 25 53.21 N	006 15 05.45 W	36.00m	39.48m	TAXI IN, PUSH OUT.	STAND 111C VACANT.	400R	53 25 29.21 N	006 14 33.73 W	36.00m	46.70m	TAXI IN, PUSH OUT.	STAND 400C VACANT. STAND 400T VACANT AT ENTRY/EXIT.
112L	53 25 54.20 N	006 15 09.17 W	36.00m	44.51m	TAXI IN, PUSH OUT.	STAND 112C VACANT.	401L	53 25 28.45 N	006 14 35.79 W	36.00m	45.10m	TAXI IN, PUSH OUT.	STAND 401C VACANT.
112C	53 25 53.11 N	006 15 08.17 W	60.30m	58.82m	TOW IN, PUSH OUT	STANDS 112L AND 112R VACANT.	401C	53 25 27.36 N	006 14 36.25 W	65.00m	63.80m	TAXI IN, PUSH OUT.	STANDS 401L, 401R VACANT.
112R	53 25 53.00 N	006 15 07.88 W	36.00m	46.50m	TAXI IN, PUSH OUT.	STAND 112C VACANT.	401R	53 25 27.23 N	006 14 37.08 W	36.00m	46.70m	TAXI IN, PUSH OUT.	STAND 401C VACANT.
113L	53 25 51.60 N	006 15 07.37 W	36.00m	46.50m	TAXI IN, PUSH OUT.	STAND 113C VACANT.	402L	53 25 26.50 N	006 14 39.18 W	36.00m	45.10m	TAXI IN, PUSH OUT.	STAND 402C VACANT.
113C*	53 25 51.71 N	006 15 06.72 W	64.80m	66.80m	TAXI IN, PUSH OUT.	STANDS 113L AND 113R VACANT.	402C	53 25 25.39 N	006 14 39.56 W	65.00m	74.00m	TAXI IN, PUSH OUT.	STANDS 402L, 402R VACANT.
113R*	53 25 50.38 N	006 15 06.18 W	36.00m	46.50m	TAXI IN, PUSH OUT.	STAND 113C VACANT.	402R	53 25 25.26 N	006 14 40.44 W	36.00m	46.70m	TAXI IN, PUSH OUT.	STAND 402C VACANT.
114L*	53 25 49.28 N	006 15 05.13 W	36.00m	46.50m	TAXI IN, PUSH OUT.	STAND 114C VACANT.	403L	53 25 24.57 N	006 14 42.61 W	36.00m	45.10m	TAXI IN, PUSH OUT.	STAND 403C VACANT.
114C*	53 25 48.96 N	006 15 05.40 W	64.80m	66.80m	TAXI IN, PUSH OUT.	STAND 114L VACANT.	403C	53 25 23.41 N	006 14 42.91 W	65.00m	74.00m	TAXI IN, PUSH OUT.	STANDS 403L, 403R VACANT.
121	53 25 48.95 N	006 15 02.61 W	36.00m	45.10m	TAXI IN, PUSH OUT.		403R	53 25 23.27 N	006 14 43.79 W	36.00m	46.70m	TAXI IN, PUSH OUT.	STAND 403C VACANT.
122	53 25 48.82 N	006 15 00.27 W	36.00m	45.10m	TAXI IN, PUSH OUT.		404L	53 25 22.58 N	006 14 45.99 W	36.00m	45.10m	TAXI IN, PUSH OUT.	STAND 404C VACANT.
123	53 25 48.69 N	006 14 57.92 W	36.00m	45.10m	TAXI IN, PUSH OUT.		404C	53 25 21.38 N	006 14 46.55 W	65.00m	74.00m	TAXI IN, PUSH OUT.	STANDS 404L, 404R VACANT.
124	53 25 48.56 N	006 14 55.57 W	36.00m	45.10m	TAXI IN, PUSH OUT.		404R	53 25 21.28 N	006 14 47.01 W	35.80m	45.10m	TAXI IN, PUSH OUT.	STAND 404C VACANT.
125	53 25 48.43 N	006 14 53.23 W	36.00m	45.10m	TAXI IN, PUSH OUT.		405A	53 25 21.63 N	006 14 39.76 W	41.40m	47.40m	TAXI IN, PUSH OUT.	STAND 405R VACANT. STAND 405A RESTRICTED TO B757-200W ONLY
126	53 25 48.30 N	006 14 50.88 W	36.00m	45.10m	TAXI IN, PUSH OUT.	STAND 200T VACANT AT ENTRY/EXIT.	405R	53 25 21.56 N	006 14 39.64 W	36.00m	44.51m	TAXI IN, PUSH OUT.	STAND 405A VACANT
127	53 25 48.17 N	006 14 48.54 W	36.00m	45.10m	TAXI IN, PUSH OUT.	STAND 200T VACANT AT ENTRY/EXIT.	406L	53 25 21.82 N	006 14 37.01 W	41.40m	47.40m	TAXI IN, PUSH OUT.	STAND 406C VACANT.
131L	53 25 55.32 N	006 14 09.13 W	36.00m	44.51m	TAXI IN, PUSH OUT.	STANDS 131C VACANT.	406C	53 25 23.12 N	006 14 36.82 W	65.00m	75.40m	TAXI IN, PUSH OUT.	STANDS 406L, 406R VACANT.
131C	53 25 55.73 N	006 14 06.82 W	65.00m	70.67m	TAXI IN, PUSH OUT.	STANDS 131L, 131R VACANT.	406R	53 25 23.28 N	006 14 36.22 W	41.40m	47.40m	TAXI IN, PUSH OUT.	STAND 406C VACANT.
131R	53 25 55.19 N	006 14 06.79 W	36.00m	44.51m	TAXI IN, PUSH OUT.	STANDS 131C VACANT.	407L	53 25 23.91 N	006 14 33.83 W	34.10m	45.10m	TAXI IN, PUSH OUT.	STAND 407C VACANT.
131S*	53 25 54.19 N	006 14 09.30 W	30.40m	30.50m	SELF MANOEUVRING.	STANDS 131L, 131R & 131C VACANT	407C	53 25 25.10 N	006 14 33.46 W	65.00m	75.40m	TAXI IN, PUSH OUT.	STANDS 407L, 407R VACANT.
132L	53 25 55.57 N	006 14 13.83 W	36.00m	44.51m	TAXI IN, PUSH OUT.	STANDS 132C VACANT.	407R	53 25 25.27 N	006 14 32.76 W	36.00m	46.70m	TAXI IN, PUSH OUT.	STAND 407C VACANT.
132C	53 25 55.98 N	006 14 11.41 W	65.00m	70.67m	TAXI IN, PUSH OUT.	STANDS 132L, 132R VACANT.	408L	53 25 25.89 N	006 14 30.48 W	36.00m	45.10m	TAXI IN, PUSH OUT.	STAND 408C VACANT.
132R	53 25 55.45 N	006 14 11.48 W	36.00m	44.51m	TAXI IN, PUSH OUT.	STANDS 132C VACANT.	408C	53 25 27.07 N	006 14 30.11 W	65.00m	75.40m	TAXI IN, PUSH OUT.	STANDS 408L, 408R VACANT.
132S*	53 25 54.44 N	006 14 13.99 W	30.40m	30.50m	SELF MANOEUVRING.	STANDS 132L, 132R & 132C VACANT.	408R	53 25 27.25 N	006 14 29.41 W	36.00m	46.70m	TAXI IN, PUSH OUT.	STAND 408C VACANT.
133L	53 25 55.83 N	006 14 18.52 W	36.00m	44.51m	TAXI IN, PUSH OUT.	STANDS 133C VACANT.	409L	53 25 27.83 N	006 14 27.06 W	36.00m	46.70m	TAXI IN, PUSH OUT.	STAND 409C VACANT AT ENTRY/EXIT
133C	53 25 56.24 N	006 14 16.11 W	65.00m	70.67m	TAXI IN, PUSH OUT.	STANDS 133L, 133R VACANT.	409C	53 25 28.94 N	006 14 25.56 W	60.30m	68.30m	TAXI IN, PUSH OUT.	STANDS 409L, 409R VACANT. USE MIN POWER ONLY. TOW ON IF A/C STOPS DURING ENTRY.
133R	53 25 55.71 N	006 14 16.17 W	36.00m	44.51m	TAXI IN, PUSH OUT.	STANDS 133C VACANT.	409R	53 25 28.81 N	006 14 25.38 W	36.00m	46.70m	TAXI IN, PUSH OUT.	STAND 409C VACANT AT ENTRY/EXIT.
133S*	53 25 54.70 N	006 14 18.69 W	30.40m	30.50m	SELF MANOEUVRING.	STANDS 133L, 133R & 133C VACANT.	411L	53 25 23.26 N	006 14 22.24 W	35.80m	44.51m	TAXI IN, PUSH OUT.	STANDS 411C VACANT.
134L	53 25 56.09 N	006 14 23.21 W	36.00m	44.51m	TAXI IN, PUSH OUT.	STANDS 134C VACANT.	411C	53 25 22.46 N	006 14 21.55 W	60.30m	63.70m	TAXI IN, PUSH OUT.	STANDS 411L, 411R VACANT.
134C	53 25 56.50 N	006 14 20.80 W	65.00m	70.67m	TAXI IN, PUSH OUT.	STANDS 134L, 134R VACANT.	411R	53 25 22.52 N	006 14 21.62 W	34.10m	37.60m	TAXI IN, PUSH OUT.	STAND 411C VACANT.
134R	53 25 55.96 N	006 14 20.86 W	36.00m	44.51m	TAXI IN, PUSH OUT.	STANDS 134C VACANT.	412	53 25 21.84 N	006 14 20.06 W	34.10m	37.60m	TAXI IN, PUSH OUT.	
134S*	53 25 54.96 N	006 14 23.38 W	30.40m	30.50m	SELF MANOEUVRING.	STANDS 134L, 134R & 134C VACANT.	413	53 25 21.24 N	006 14 18.04 W	34.10m	37.60m	TAXI IN, PUSH OUT.	
135L	53 25 56.36 N	006 14 27.90 W	36.00m	44.51m	TAXI IN, PUSH OUT.	STANDS 135C VACANT.	414	53 25 20.61 N	006 14 16.05 W	34.10m	37.60m	TAXI IN, PUSH OUT.	
135C	53 25 56.76 N	006 14 25.49 W	65.00m	70.67m	TAXI IN, PUSH OUT.	STANDS 135L, 135R VACANT.	415	53 25 19.92 N	006 14 14.04 W	36.00m	44.51m	TAXI IN, PUSH OUT.	
135R	53 25 56.22 N	006 14 25.56 W	36.00m	44.51m	TAXI IN, PUSH OUT.	STANDS 135C VACANT.	416	53 25 19.10 N	006 14 12.10 W	36.00m	44.51m	TAXI IN, PUSH OUT.	
135S*	53 25 55.22 N	006 14 28.07 W	30.40m	30.50m	SELF MANOEUVRING.	STANDS 135L, 135R & 135C VACANT.	417	53 25 18.38 N	006 14 09.98 W	36.00m	37.60m	TAXI IN, PUSH OUT.	
136L	53 25 57.03 N	006 14 32.53 W	36.00m	44.51m	TAXI IN, PUSH OUT.	STAND 136S VACANT	418	53 25 16.96 N	006 14 07.02 W	36.00m	44.51m	TAXI IN, PUSH OUT.	
136R	53 25 56.71 N	006 14 30.21 W	36.00m	44.51m	TAXI IN, PUSH OUT.	STAND 136S VACANT	605A	53 25 36.44 N	006 15 41.45 W	36.00			